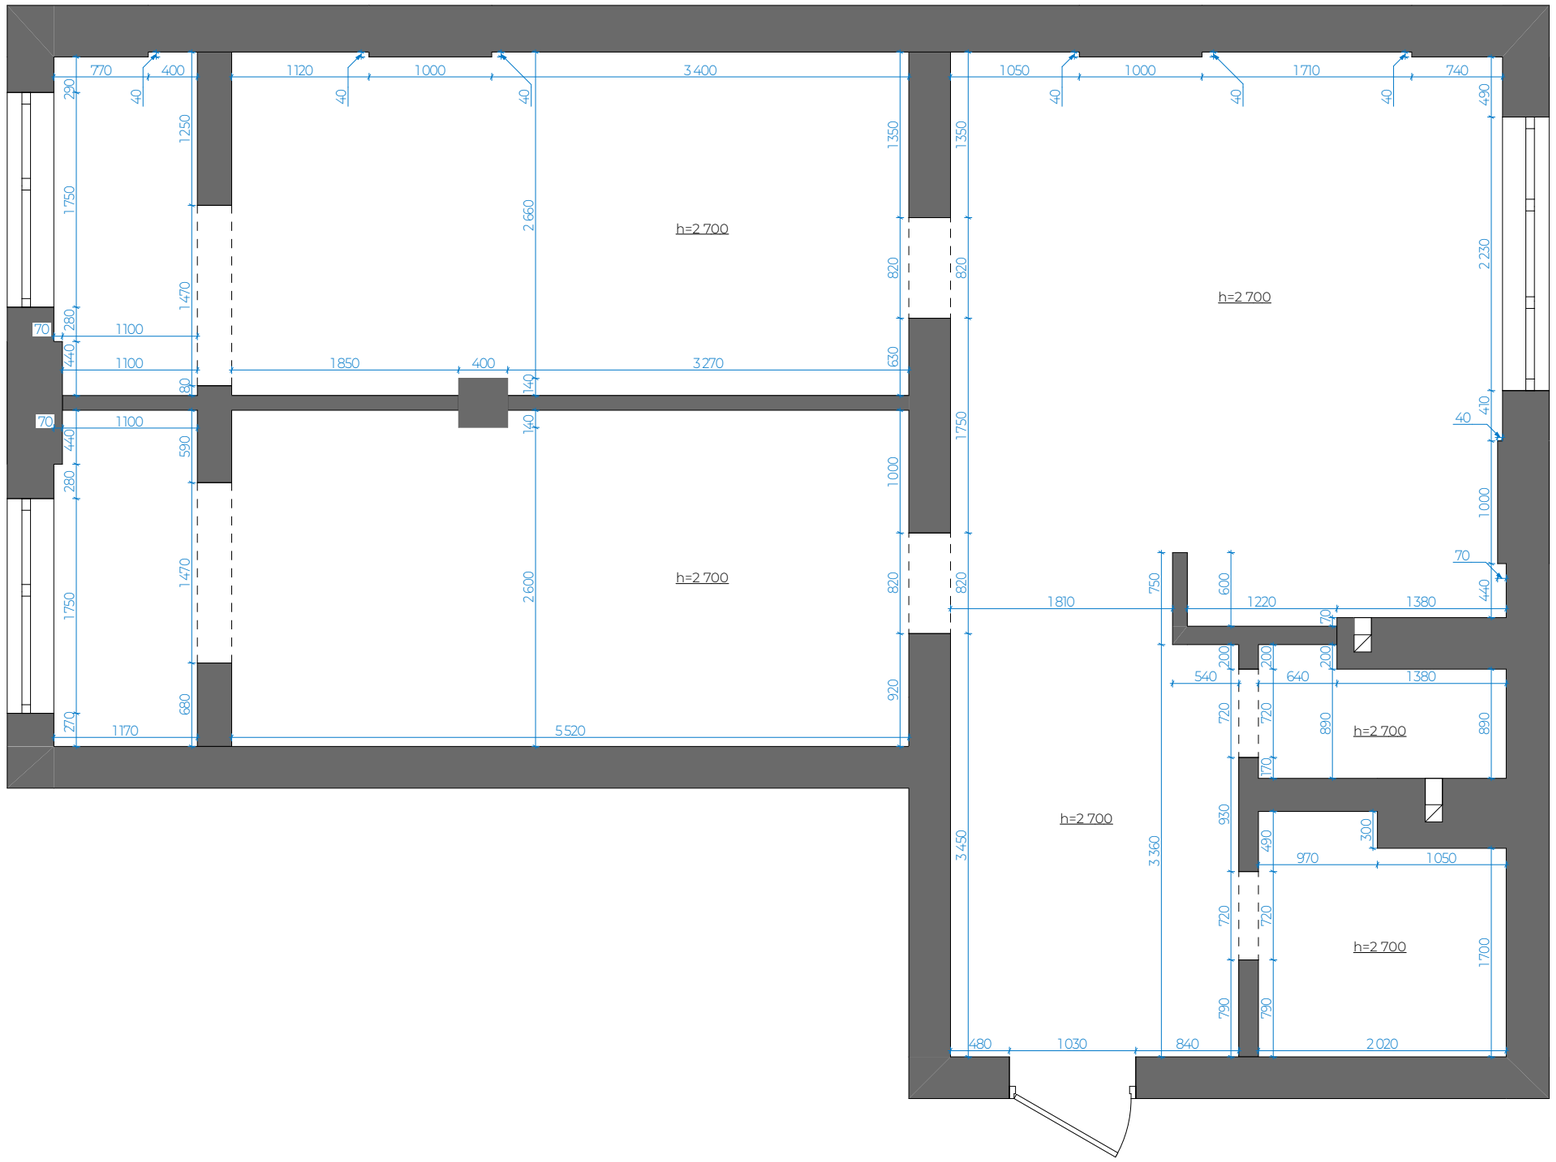

Примітки :

1. На плані вказані розміри з допустимою похибкою +/- 15мм.
2. Загальна площа обмірного плану квартири - 75,46 м.кв

ПЛАН ДЕМОНТАЖУ

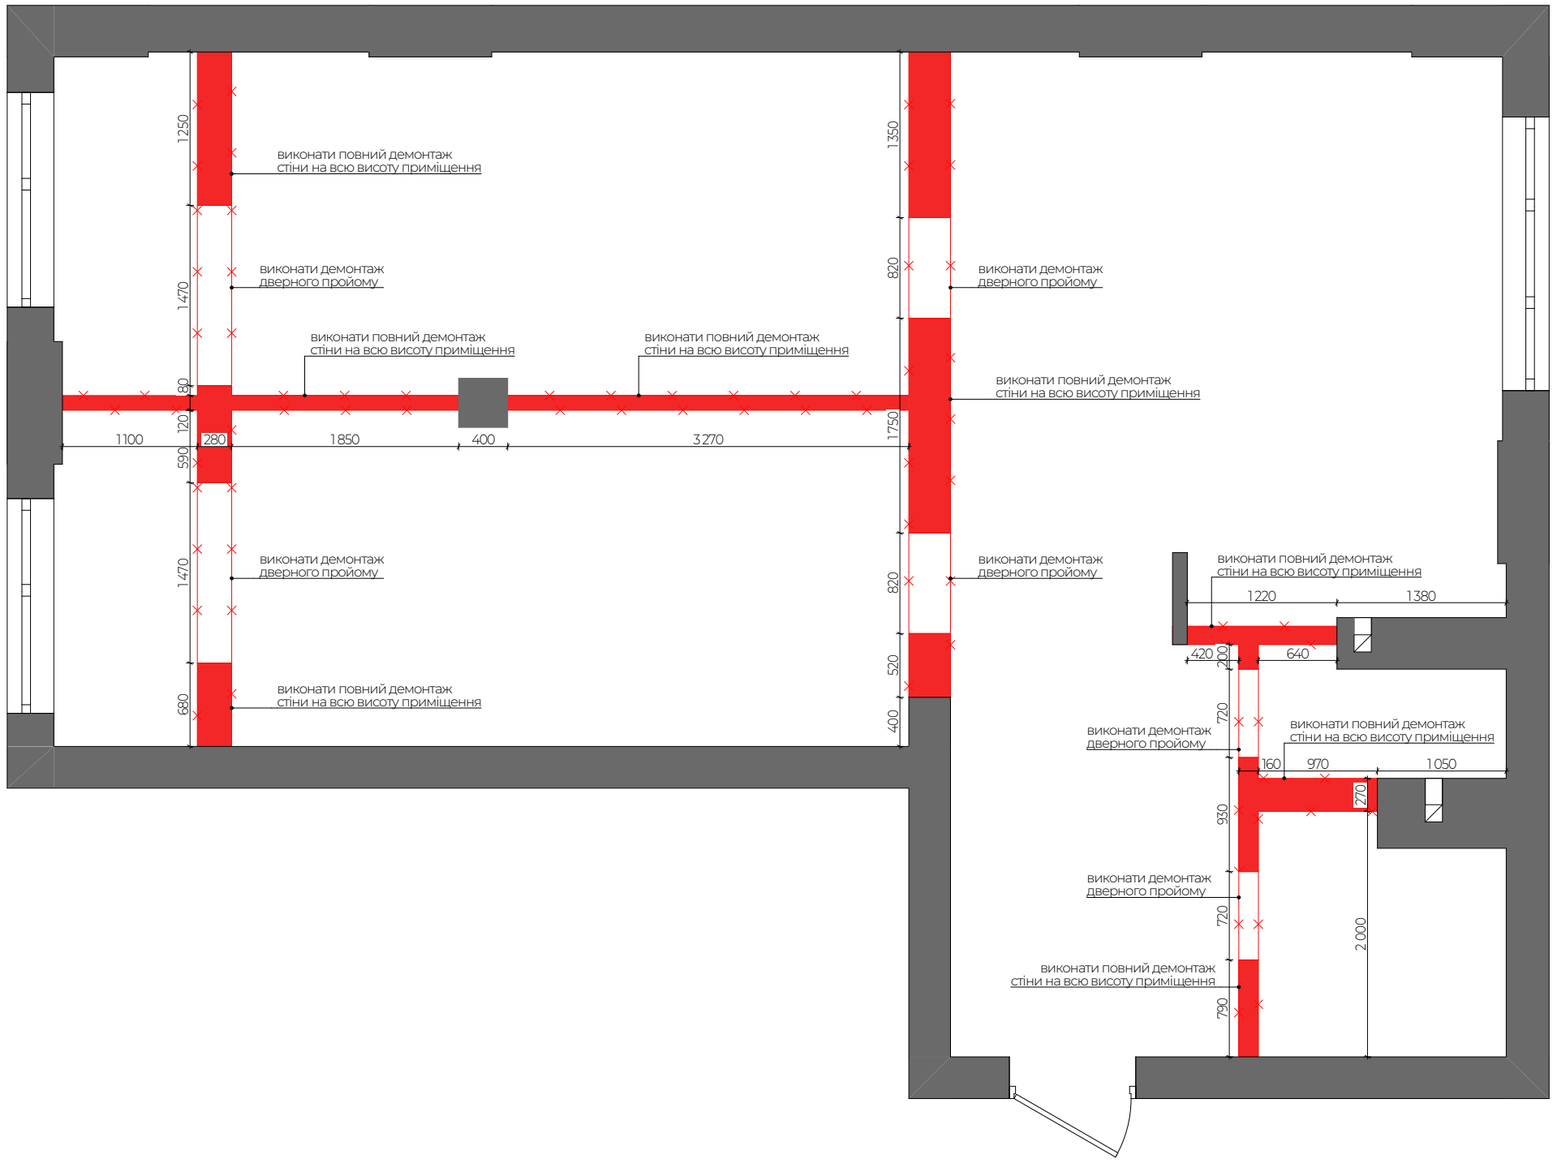

Умовні позначення:

- існуючі стіни
- демонтаж стін
- демонтаж об'єктів

Примітки :

1. Зміст та загальні дані див. аркуш ДЗ-3.
2. Розміри приміщень після перепланування уточнити згідно арк. ДЗ-16.
3. За відм. 0.000 взяти рівень "чистої" підлоги.

1-1

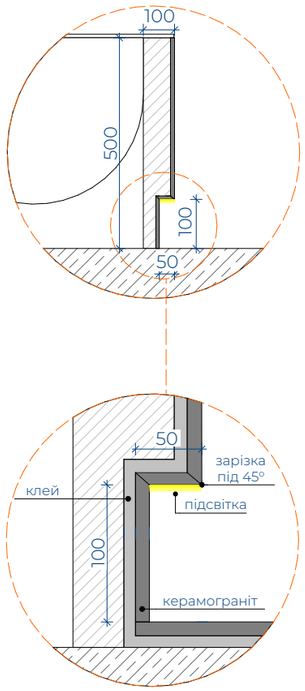

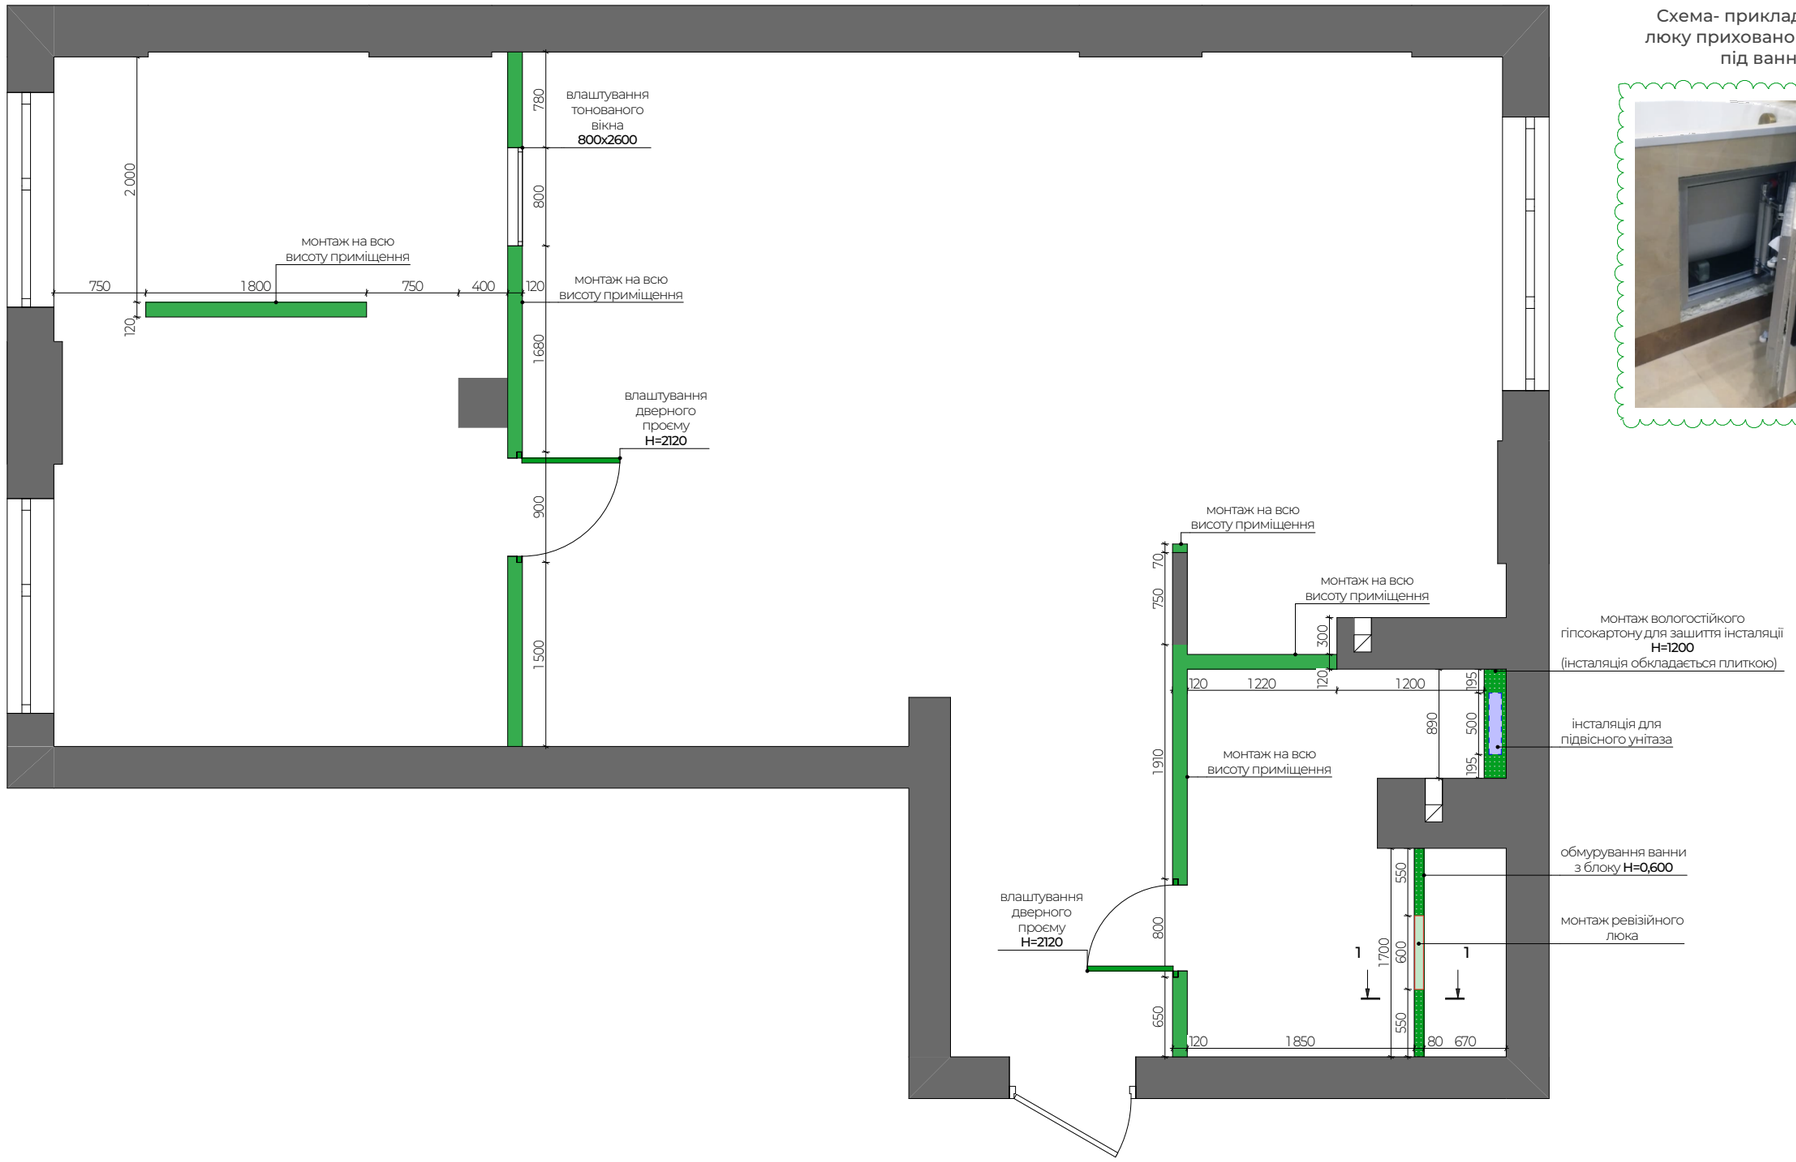

Схема- приклад монтажу
люку прихованого монтажу
під ванною

Примітки :

1. За відм. 0.000 взяти рівень "чистої" підлоги.
2. Товщини монтованих стін вказані без врахування вирівнювання стін.

ПЛАН ВЛАШТУВАННЯ СИСТЕМИ ОПАЛЕННЯ

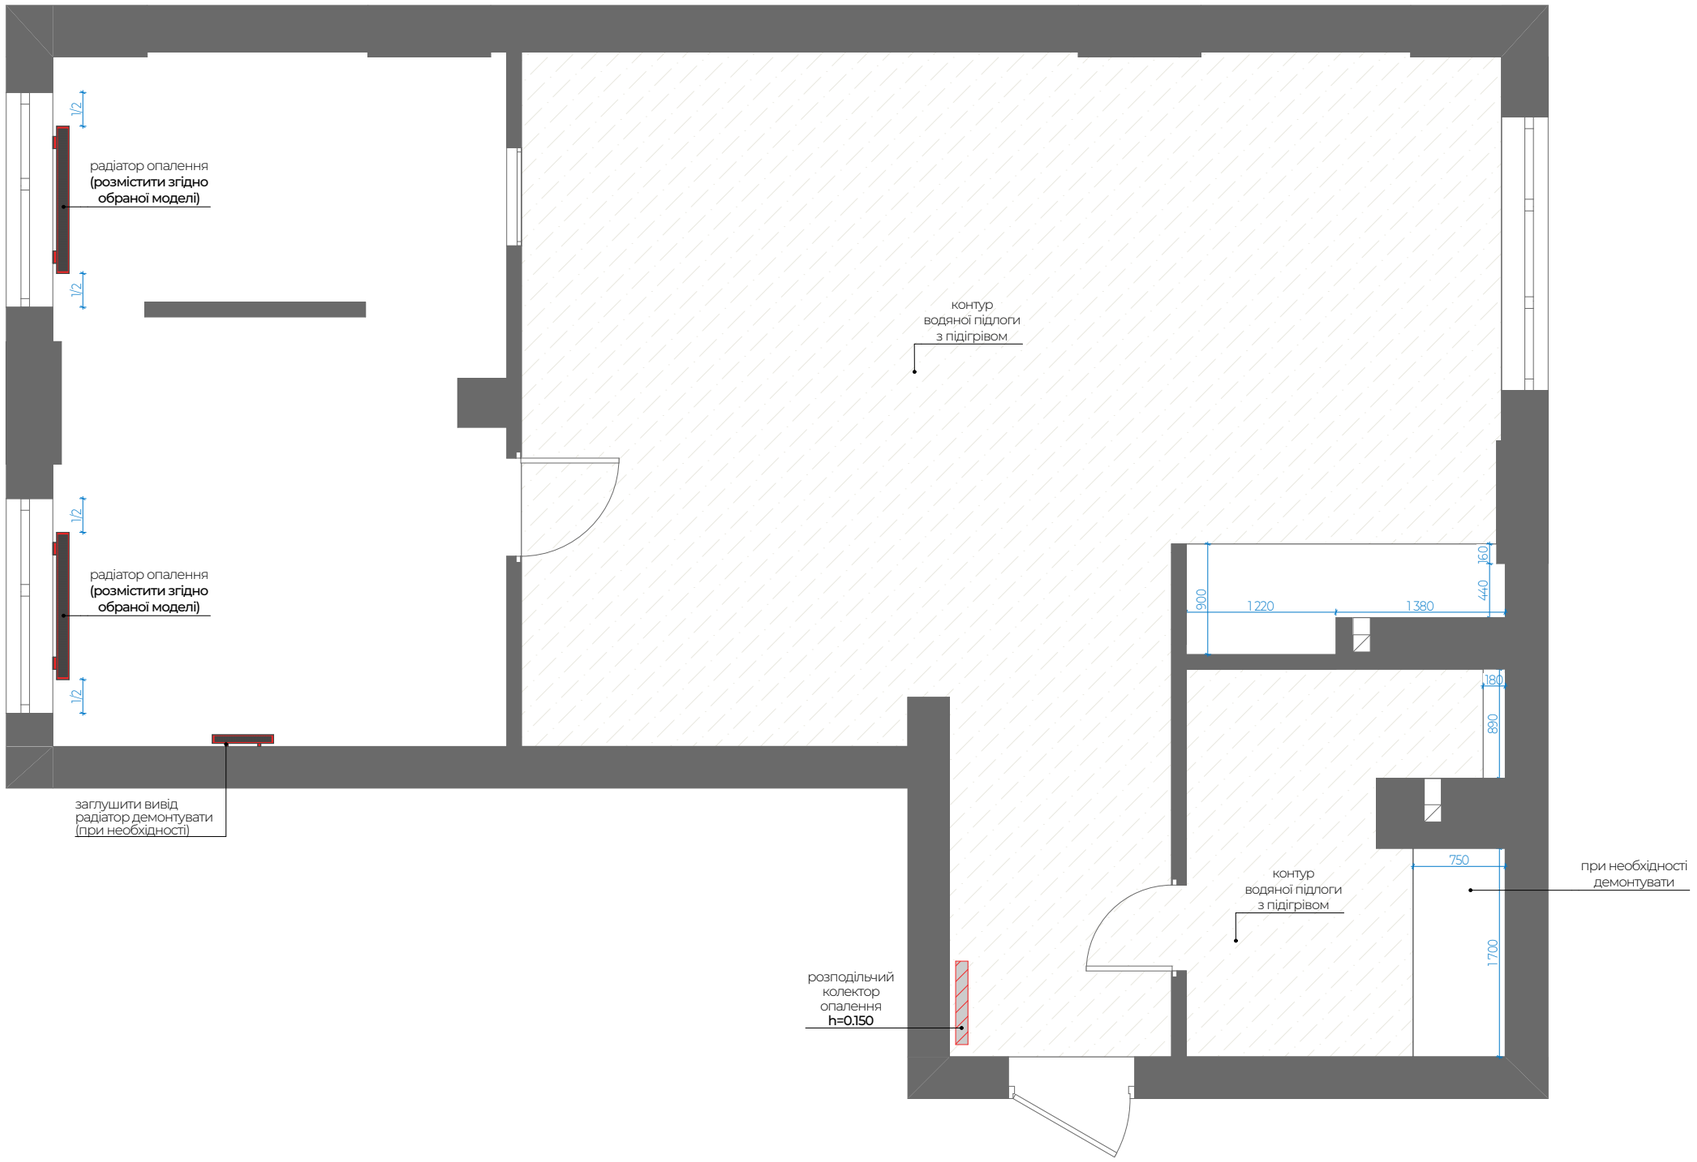

Позначення на плані	
Найменування	контур водяної підлоги з підігрівом
Площа м2	51,39

Примітки :
1. Зміст та загальні дані див. аркуш ДЗ-3.
2. За відм. 0.000 взяти рівень "чистої" підлоги.