





Примітки :

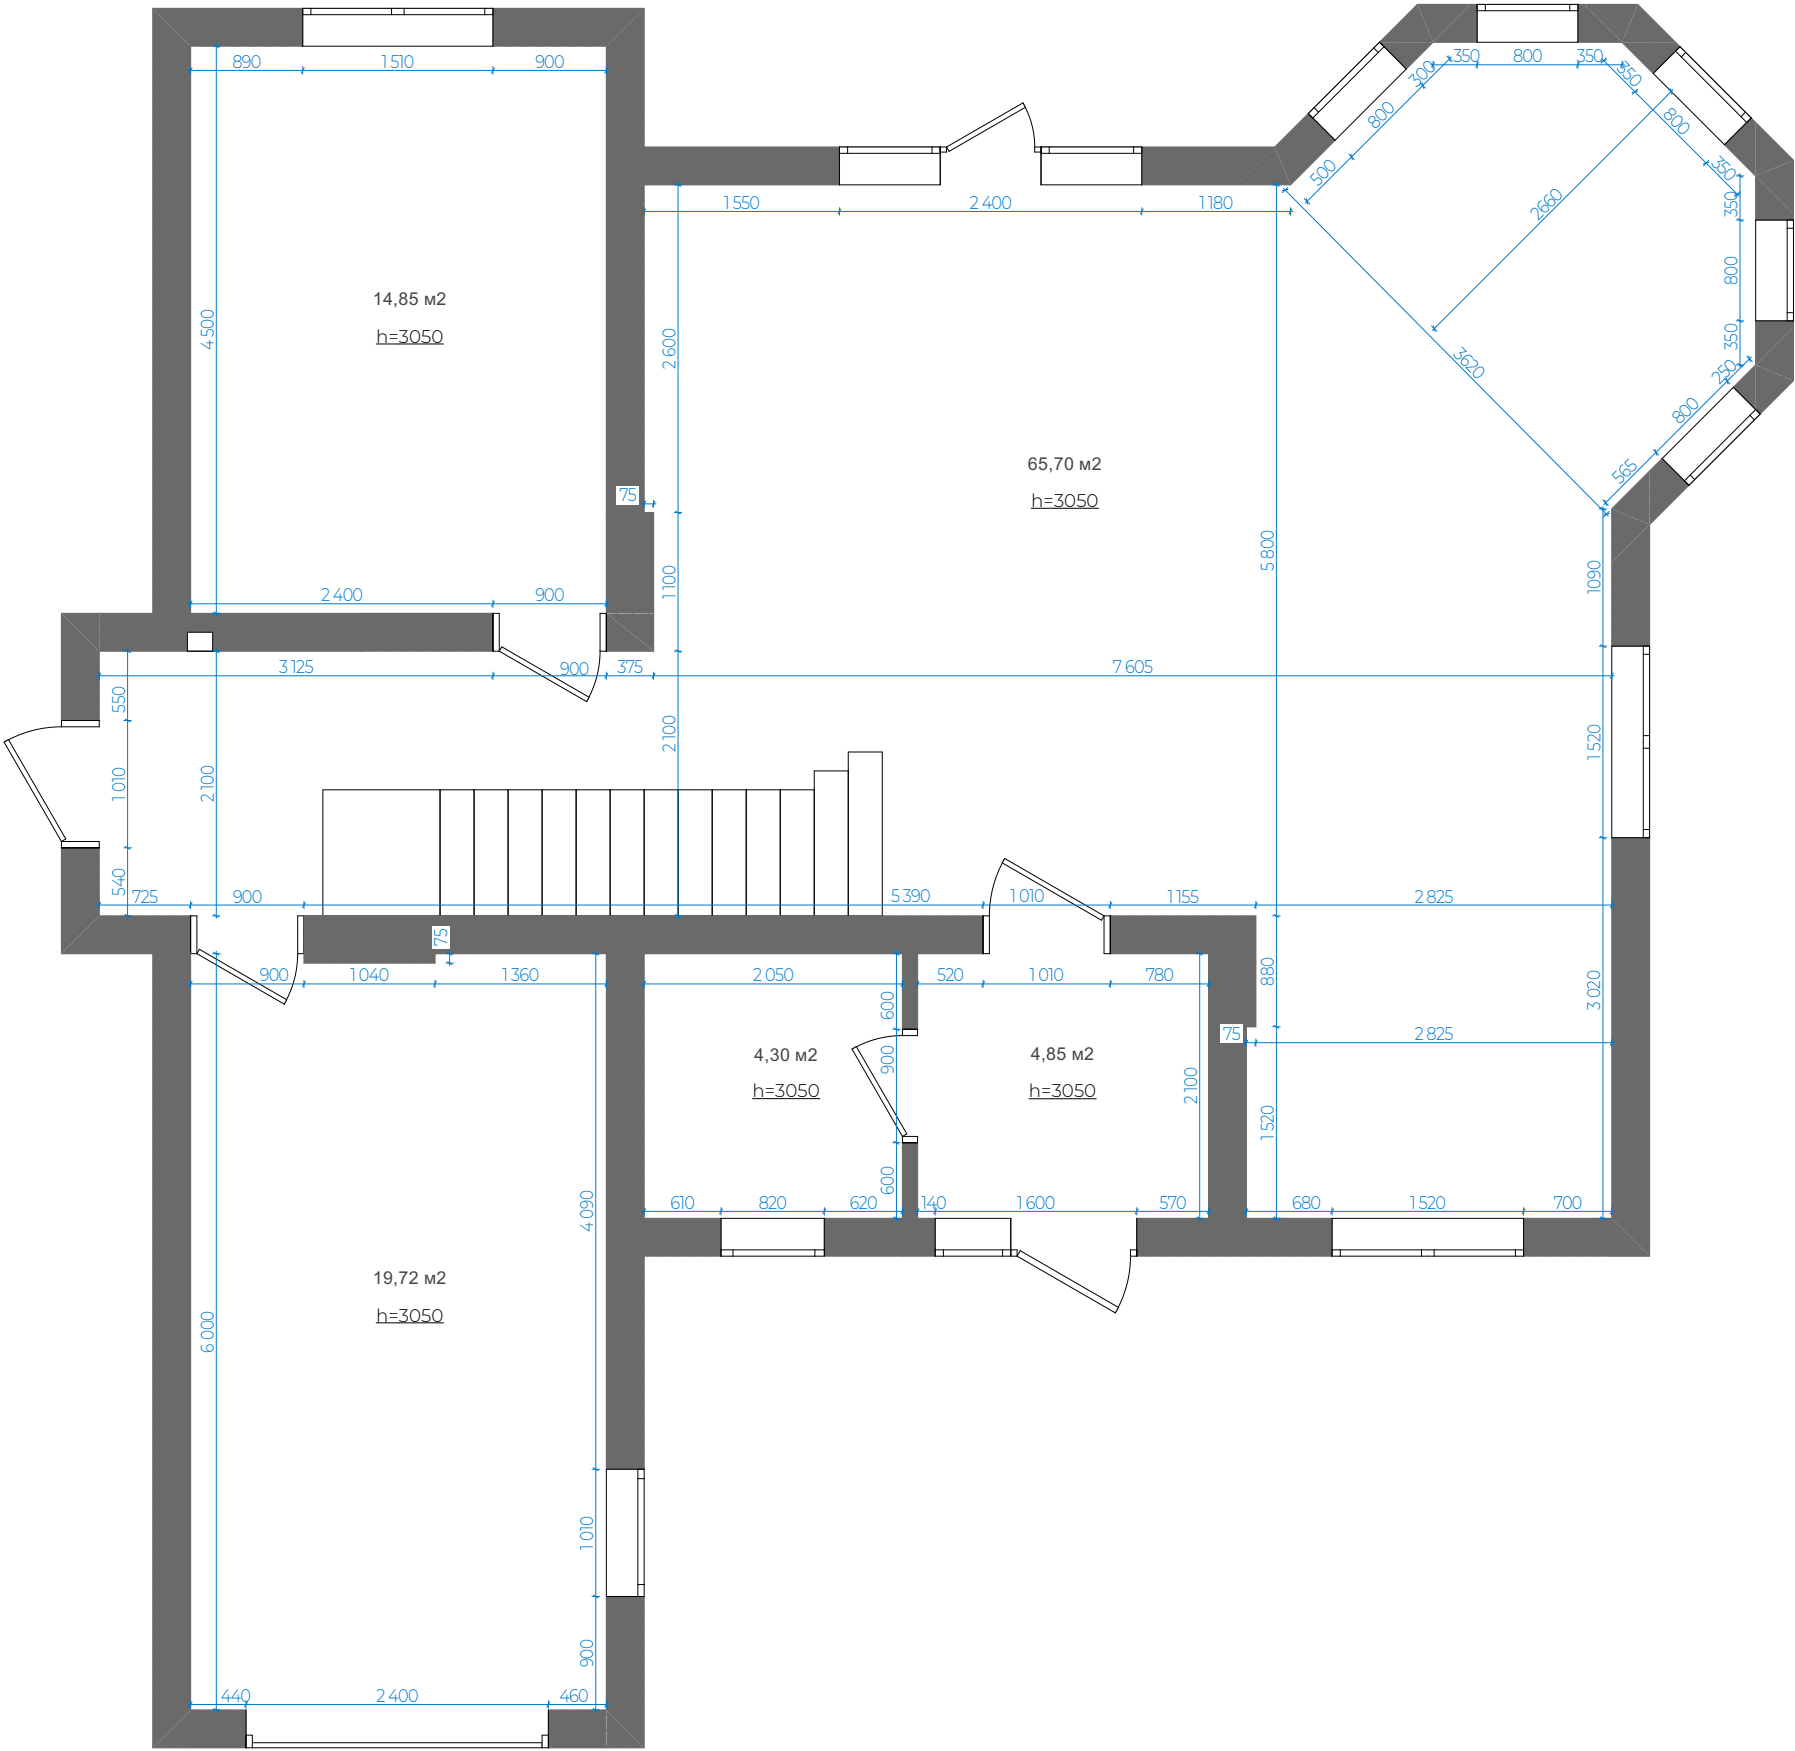


Примітки :

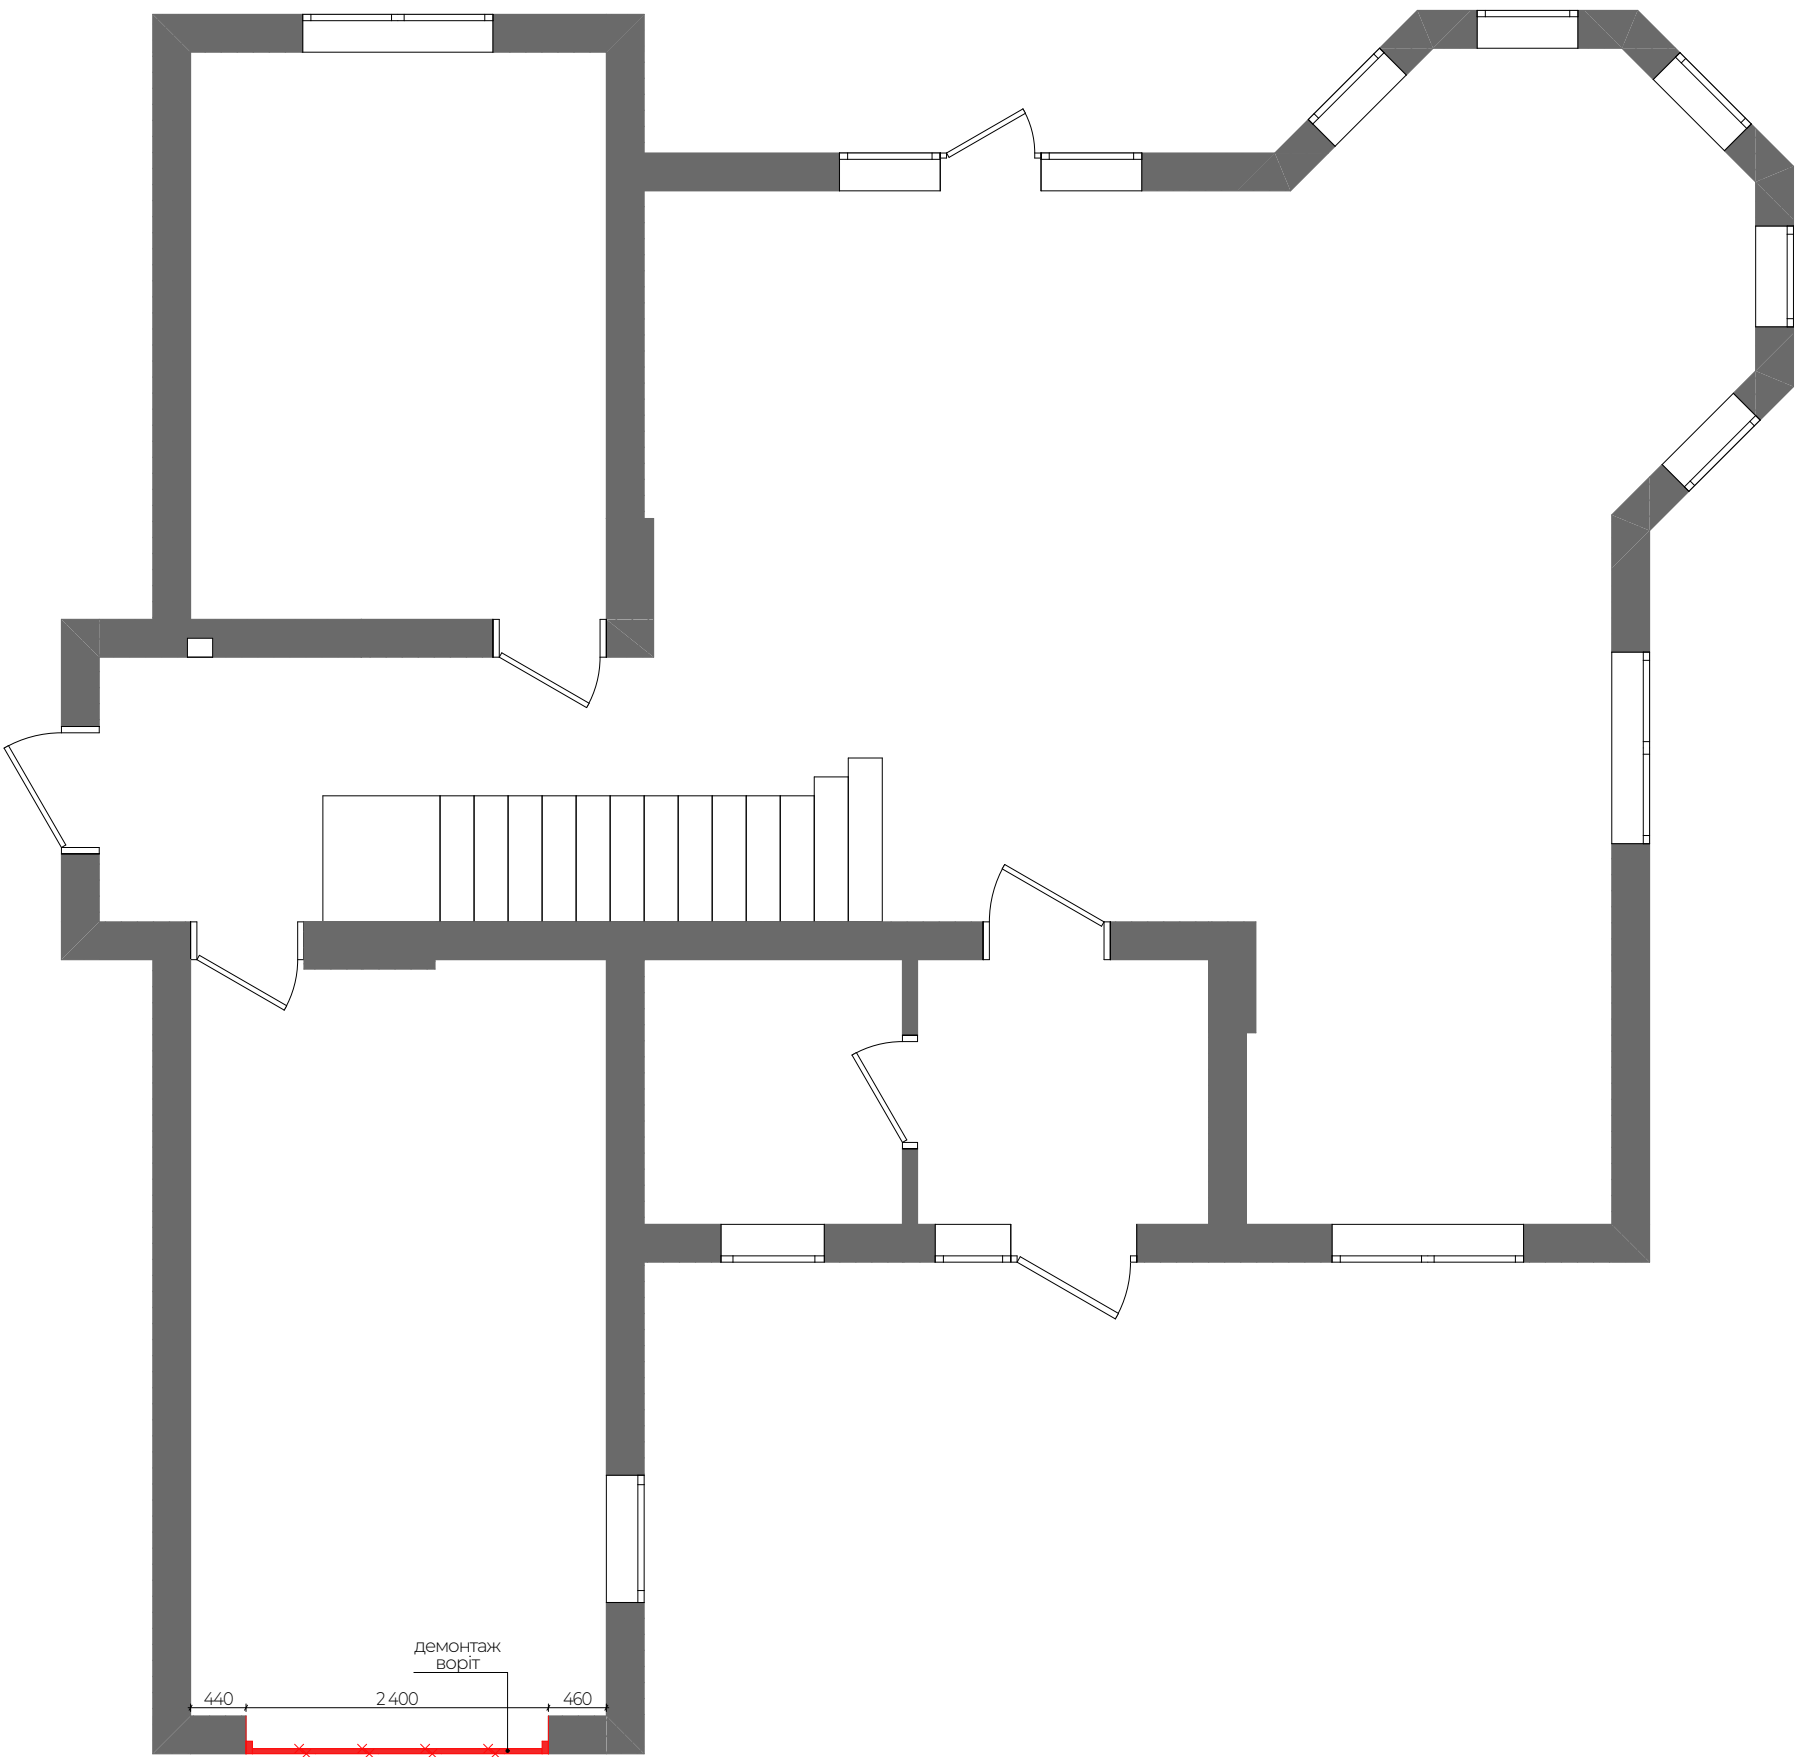

Умовні позначення:

- існуючі стіни
- демонтаж стін
- демонтажні роботи
- демонтаж об'єктів


Примітки : 1. Зміст та загальні дані див. аркуш ДЗ-3.
2. Розміри приміщень після перепланування уточнити згідно арк. ДЗ-16.
3. За відм. 0.000 взяти рівень "чистої" підлоги.

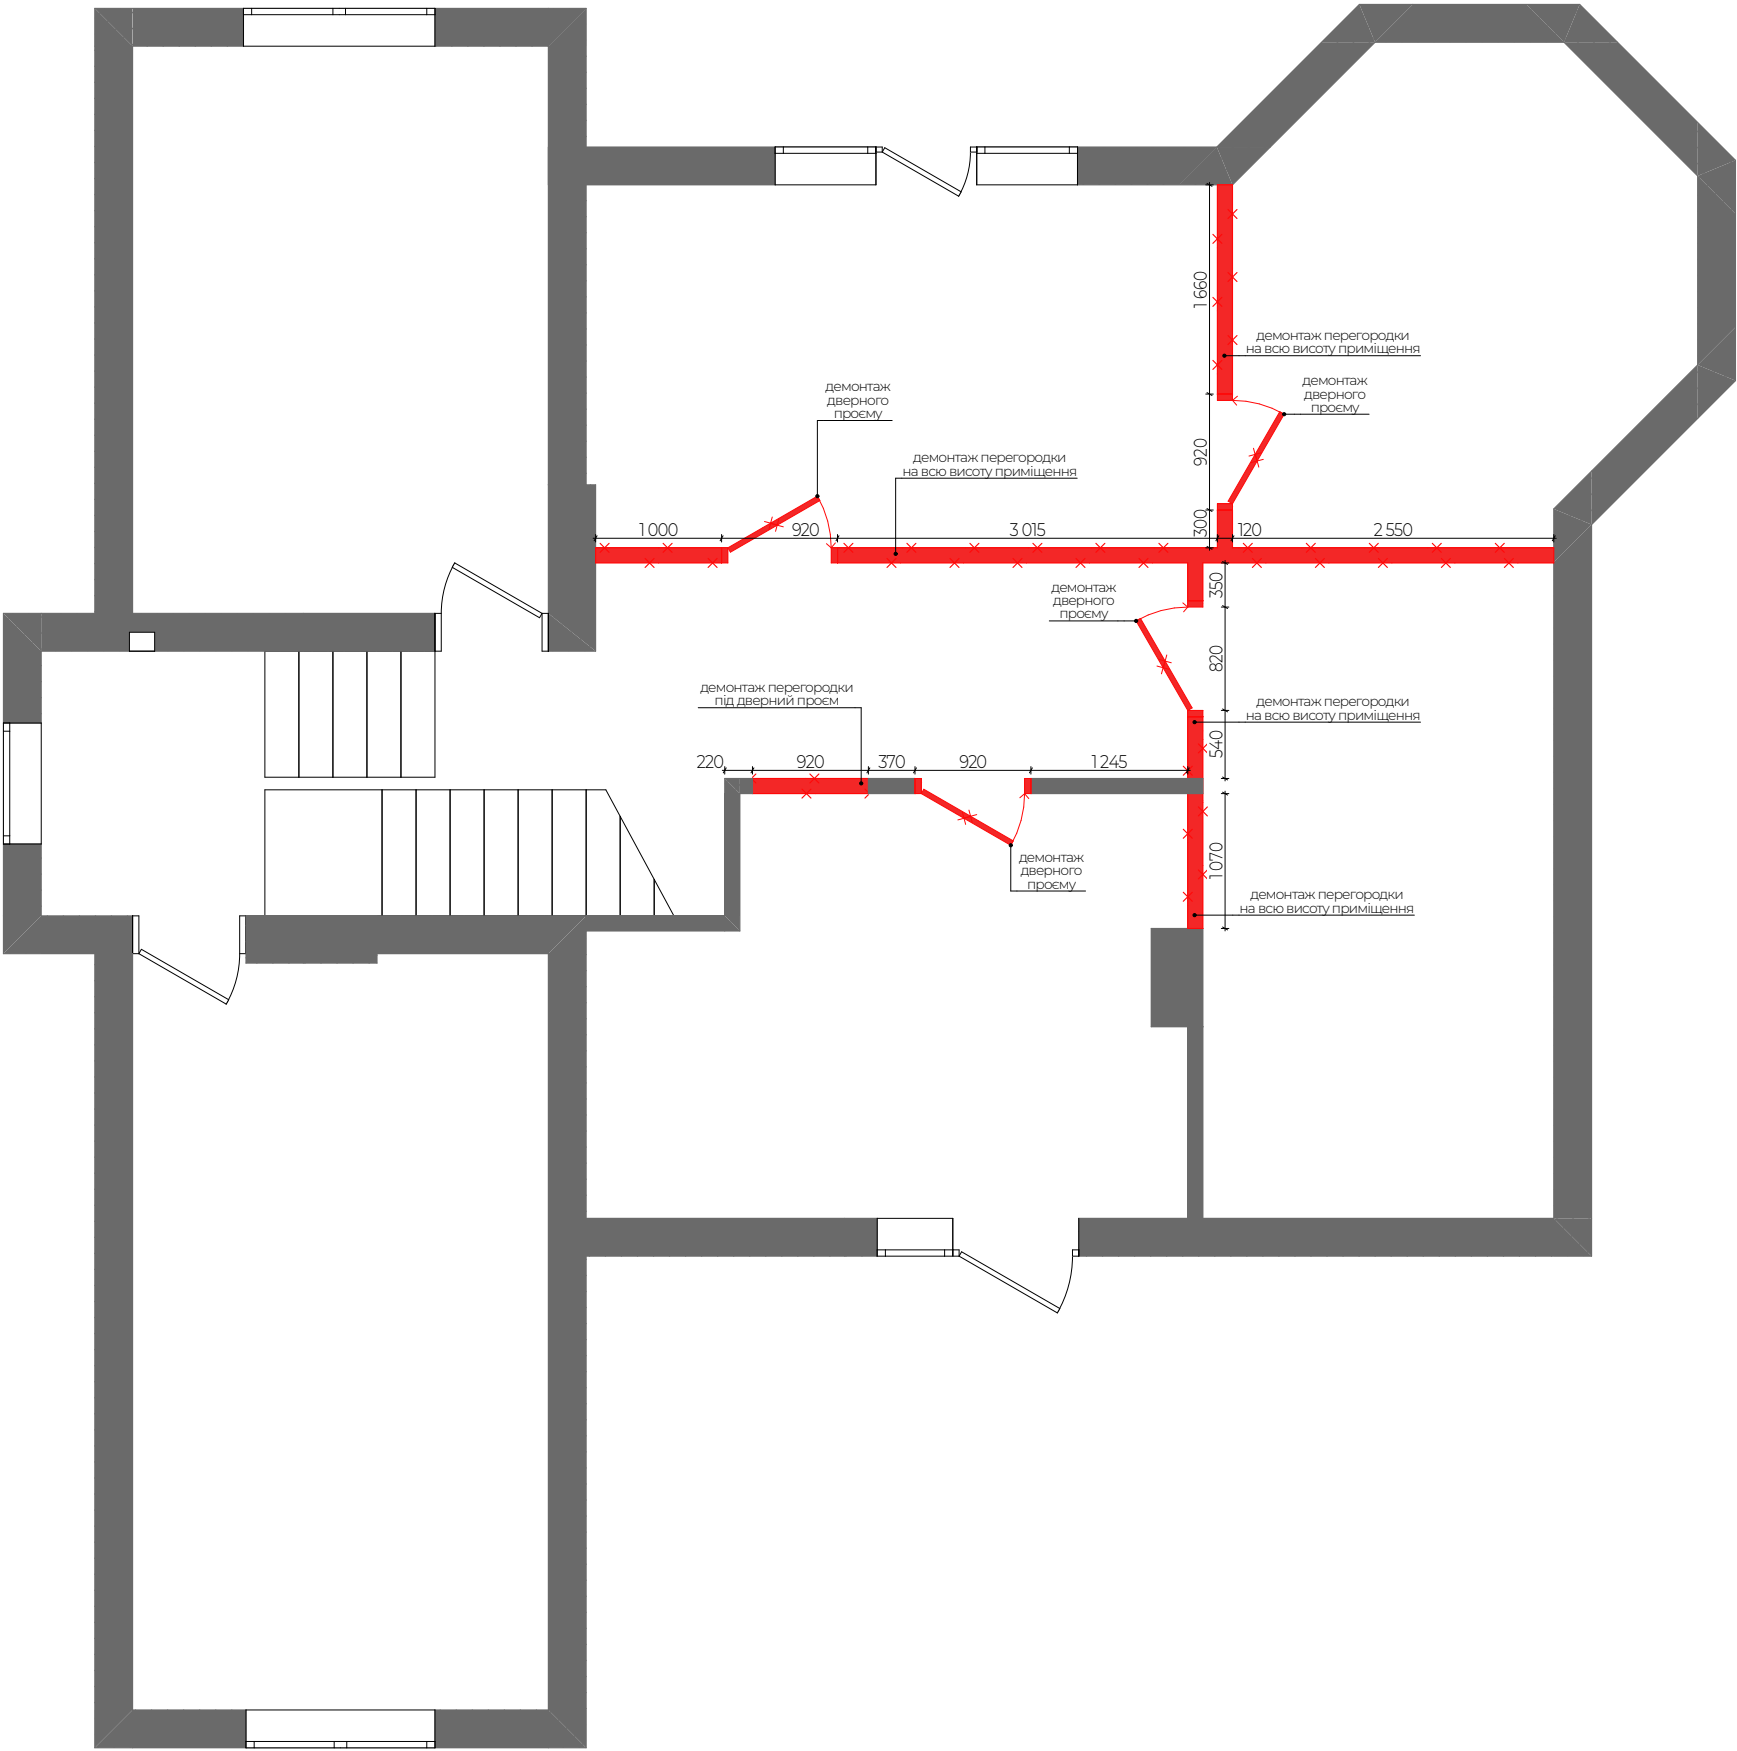

Умовні позначення:

- існуючі стіни
- демонтаж стін
- демонтажні роботи
- демонтаж об'єктів


Примітки : 1. Зміст та загальні дані див. аркуш ДЗ-3.
2. Розміри приміщень після перепланування уточнити згідно арк. ДЗ-16.
3. За відм. 0.000 взяти рівень "чистої" підлоги.

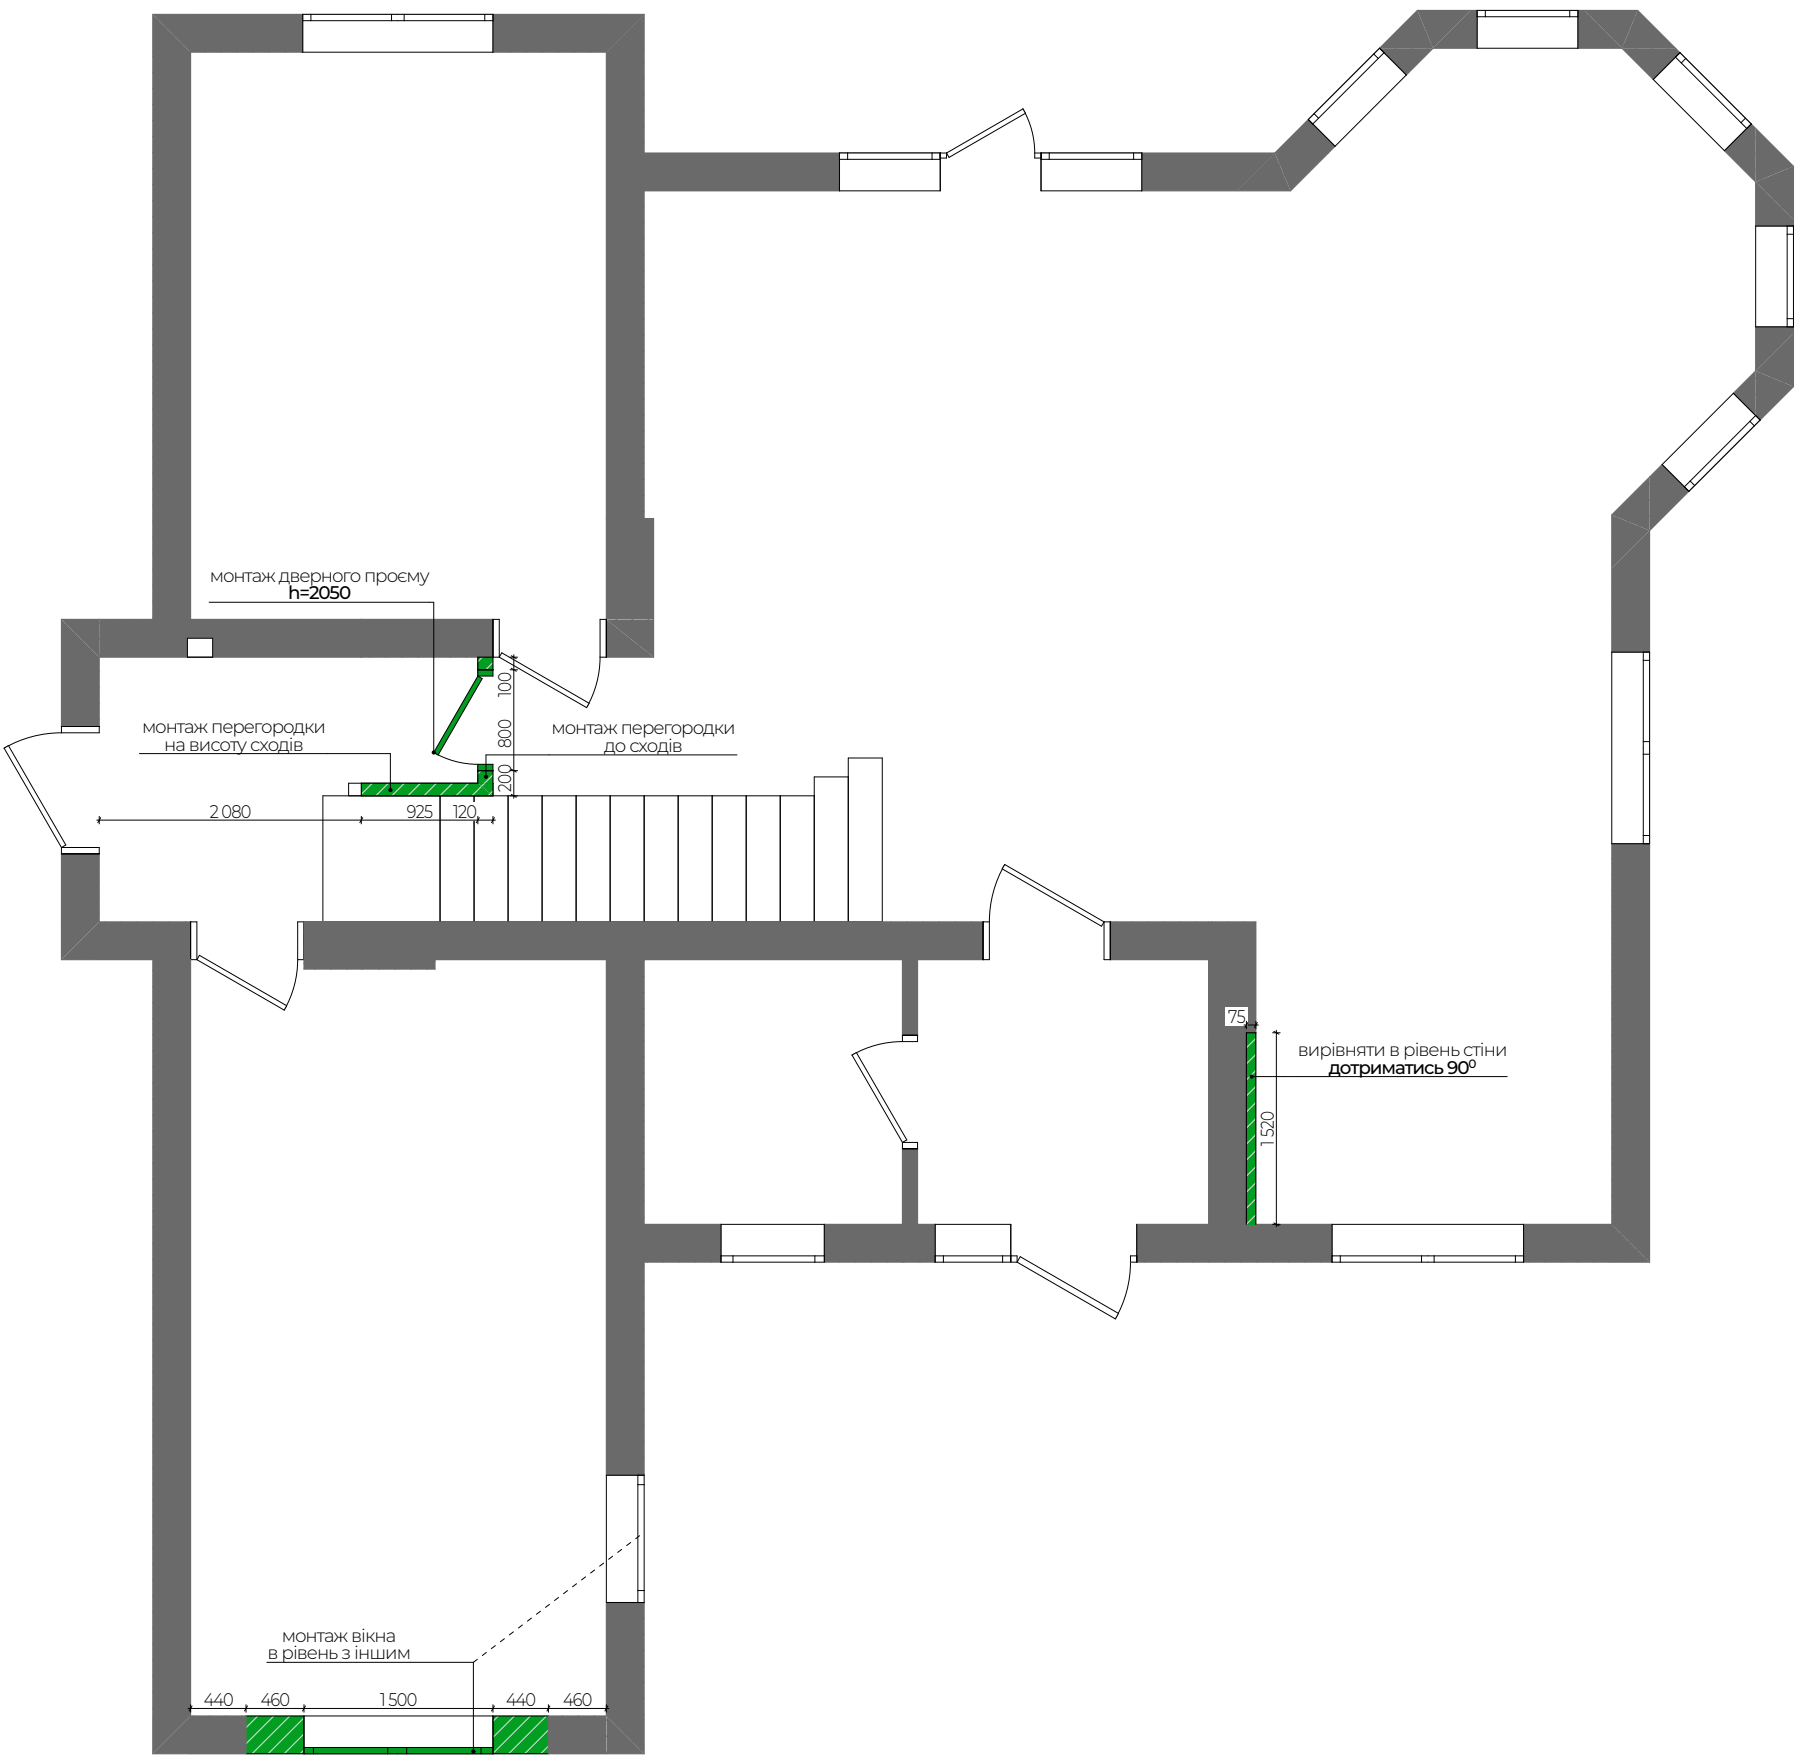

Умовні позначення:

- існуючі стіни
- монтаж перегородки


Примітки : 1. За відм. 0.000 взяти рівень "чистої" підлоги.
2. Товщини монтованих стін вказані без врахування вирівнювання стін.

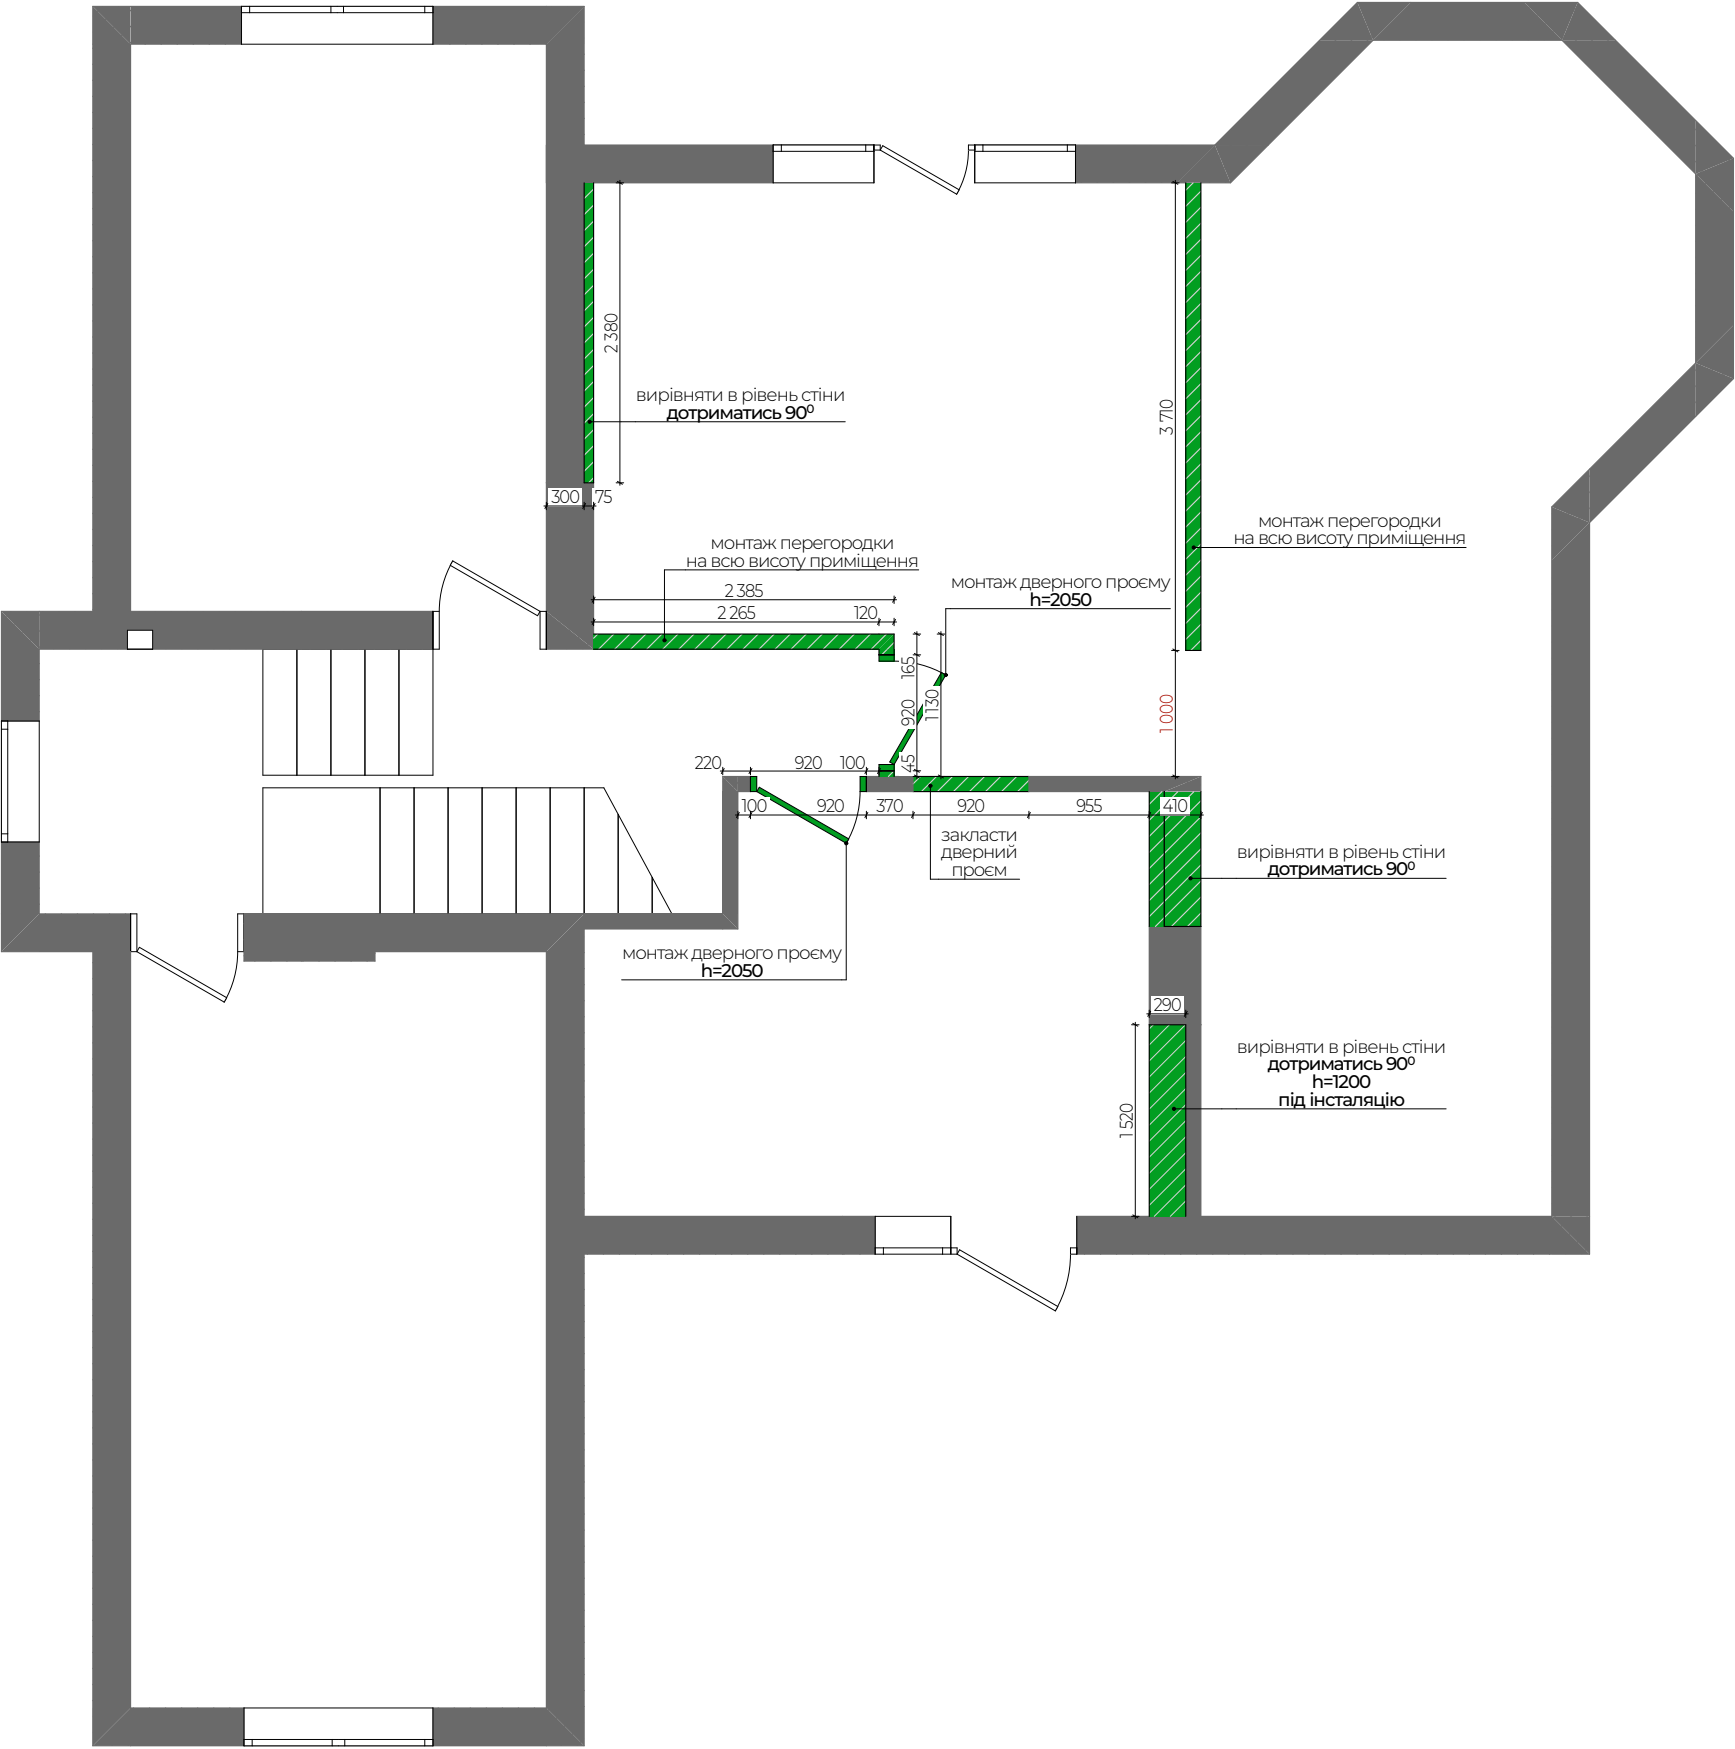

Умовні позначення:

- існуючі стіни
- монтаж перегородки

Примітки : 1. За відм. 0.000 взяти рівень "чистої" підлоги.
2. Товщини монтованих стін вказані без врахування вирівнювання стін.

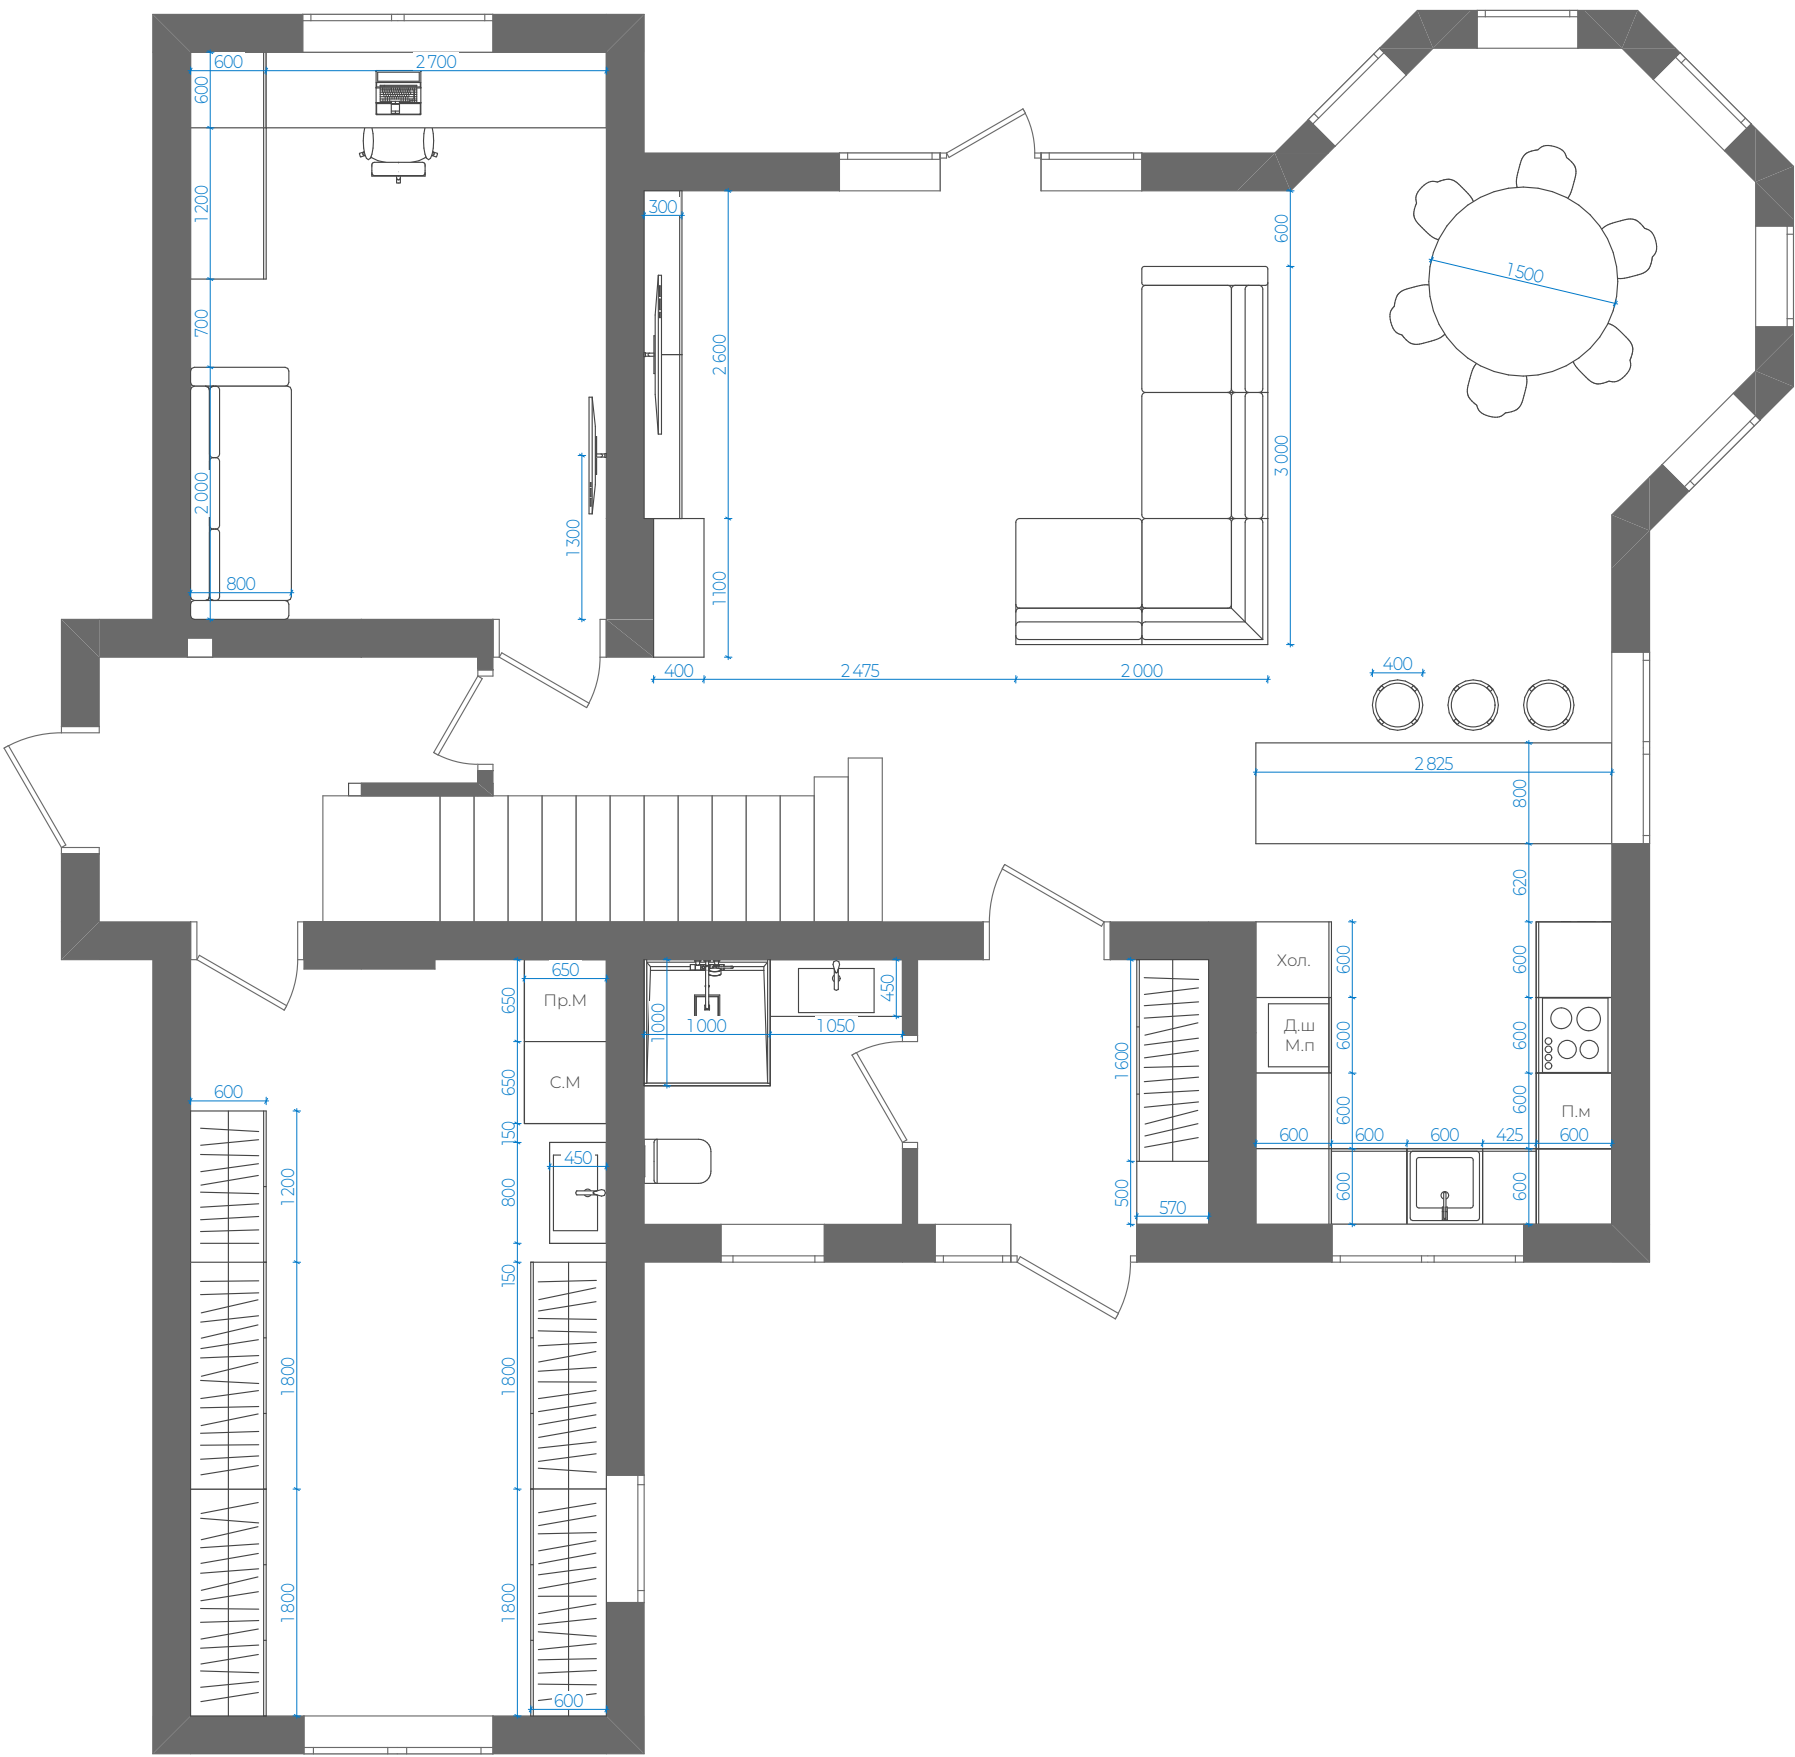

Експлікація приміщень:

1	Коридор	4,85
2	Душова	4,30
3	Кухня-вітальня	65,70
4	Гостьова	14,85
5	Гардероб	19,72

Примітки : 1. На плані вказані розміри з допустимою похибкою +/- 15мм.
2. Загальна площа виконання дизайн проекту - 214,4 м2. 109,42 м²



Експлікація приміщень:


1	Дитяча 1	19,72
2	Дитяча 2	14,85
3	Сходово	5,08
4	Коридор	9,32
5	Ванна	14,39
6	Спальня 1	14,54
7	Спальня 2	14,48
8	Горище	12,60

Примітки :


1. На плані вказані розміри з допустимою похибкою +/- 15мм.

2. Загальна площа виконання дизайн проекту - 214,4 м2.

104,98 м²

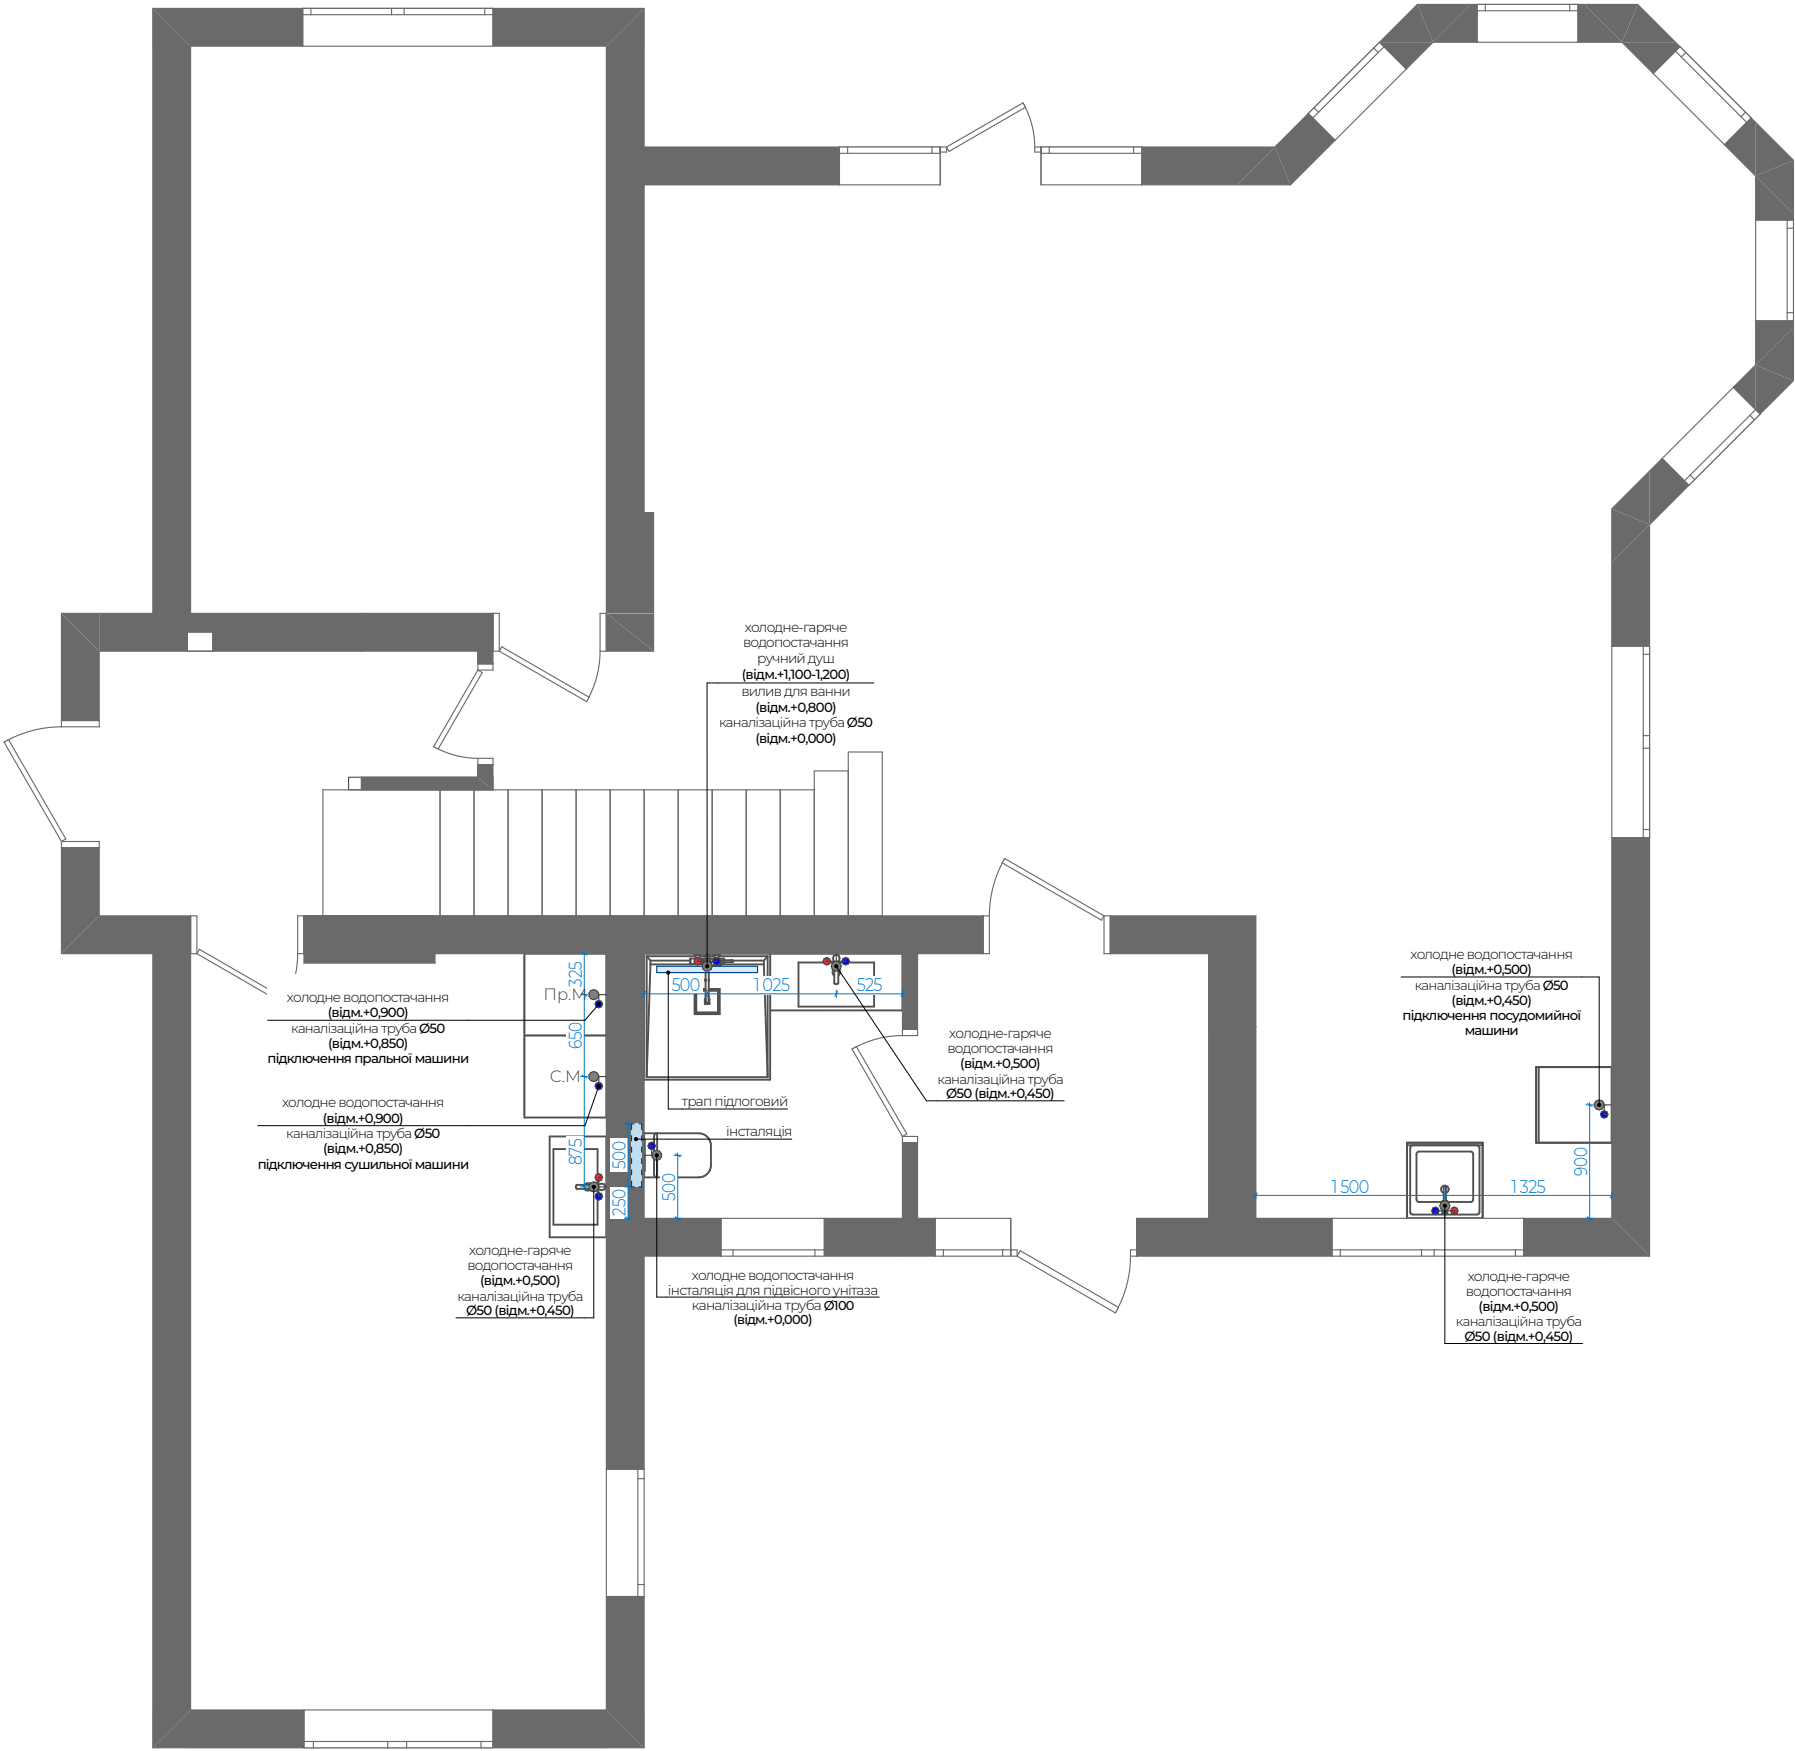

- Примітки :
- 1. Розташування сантехнічних приладів відповідає виконаним фотореалістичним візуалізаціям.
 - 2. На плані вказано прив'язки осей сантехнічних приладів та каналізаційних труб з відмітками до центру виводів.
 - 3. Відомість сантехнічних приладів додана в кінці альбому.
 - 4. За відм. 0.000 взяти рівень "чистої" підлоги.

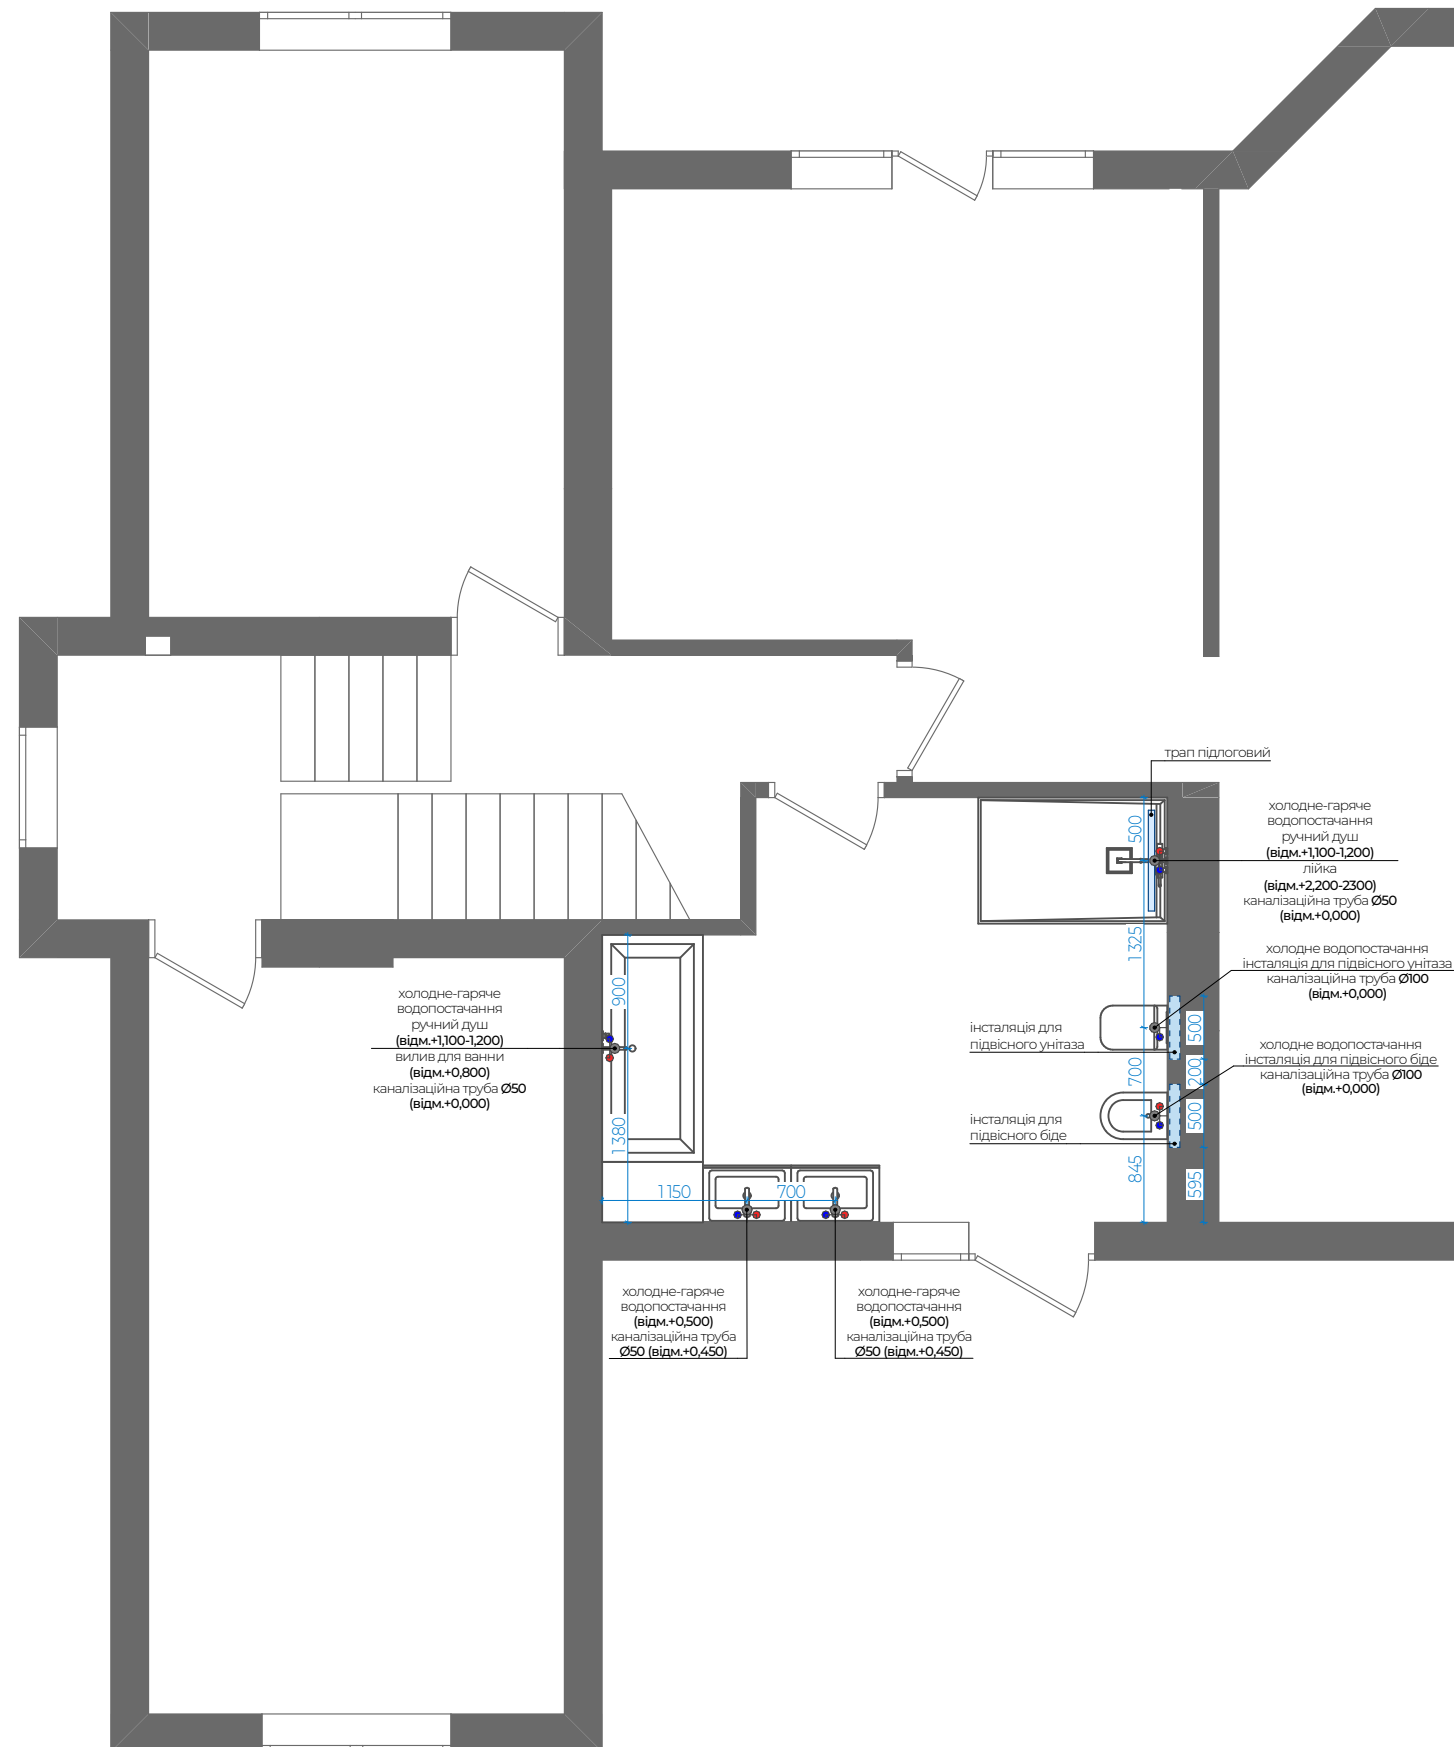

1. Розташування сантехнічних приладів відповідає виконаним фотореалістичним візуалізаціям.
2. На плані вказано прив'язки осей сантехнічних приладів та каналізаційних труб з відмітками до центру виводів.
3. Відомість сантехнічних приладів додана в кінці альбому.
4. За відм. 0.000 взяти рівень "чистої" підлоги.

Примітки: 4. За відм. 0.000 взяти рівень "чистої" підлоги.