
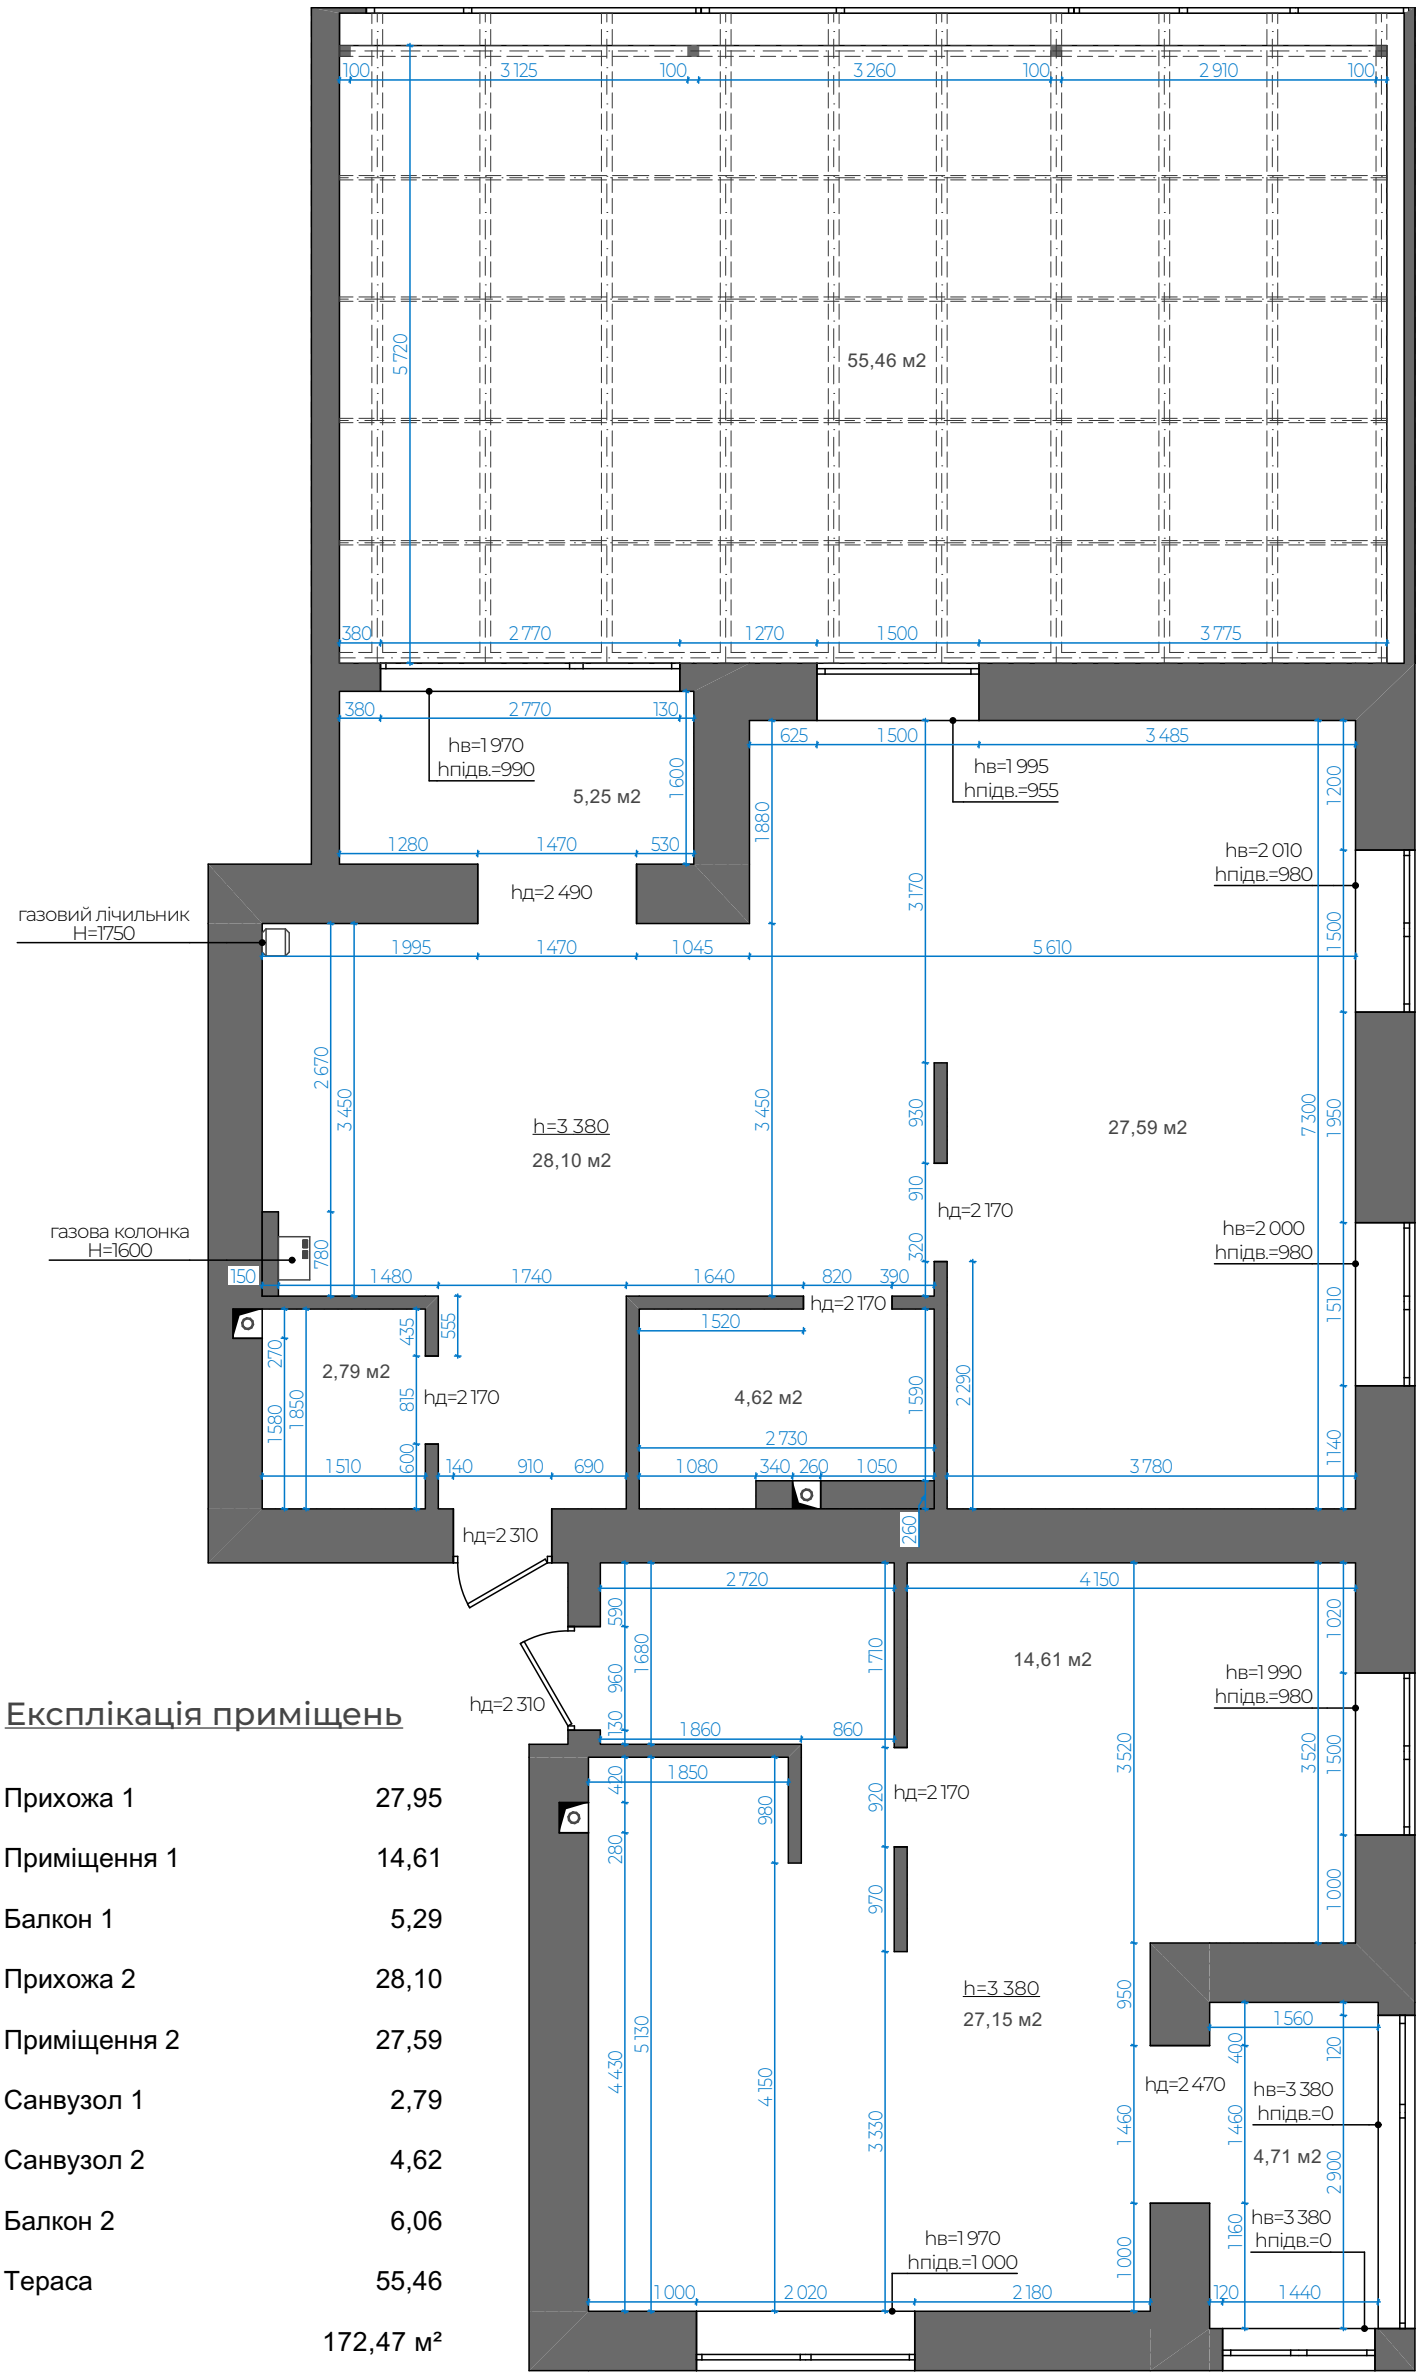



Експлікація приміщень

1	Прихожа 1	27,95
2	Приміщення 1	14,61
3	Балкон 1	5,29
4	Прихожа 2	28,10
5	Приміщення 2	27,59
6	Санвузол 1	2,79
7	Санвузол 2	4,62
8	Балкон 2	6,06
9	Тераса	55,46
		172,47 м²

Примітки :
1. Зміст та загальні дані див. аркуш ДЗ-3.
3. Допустима похибка 15-20 мм.

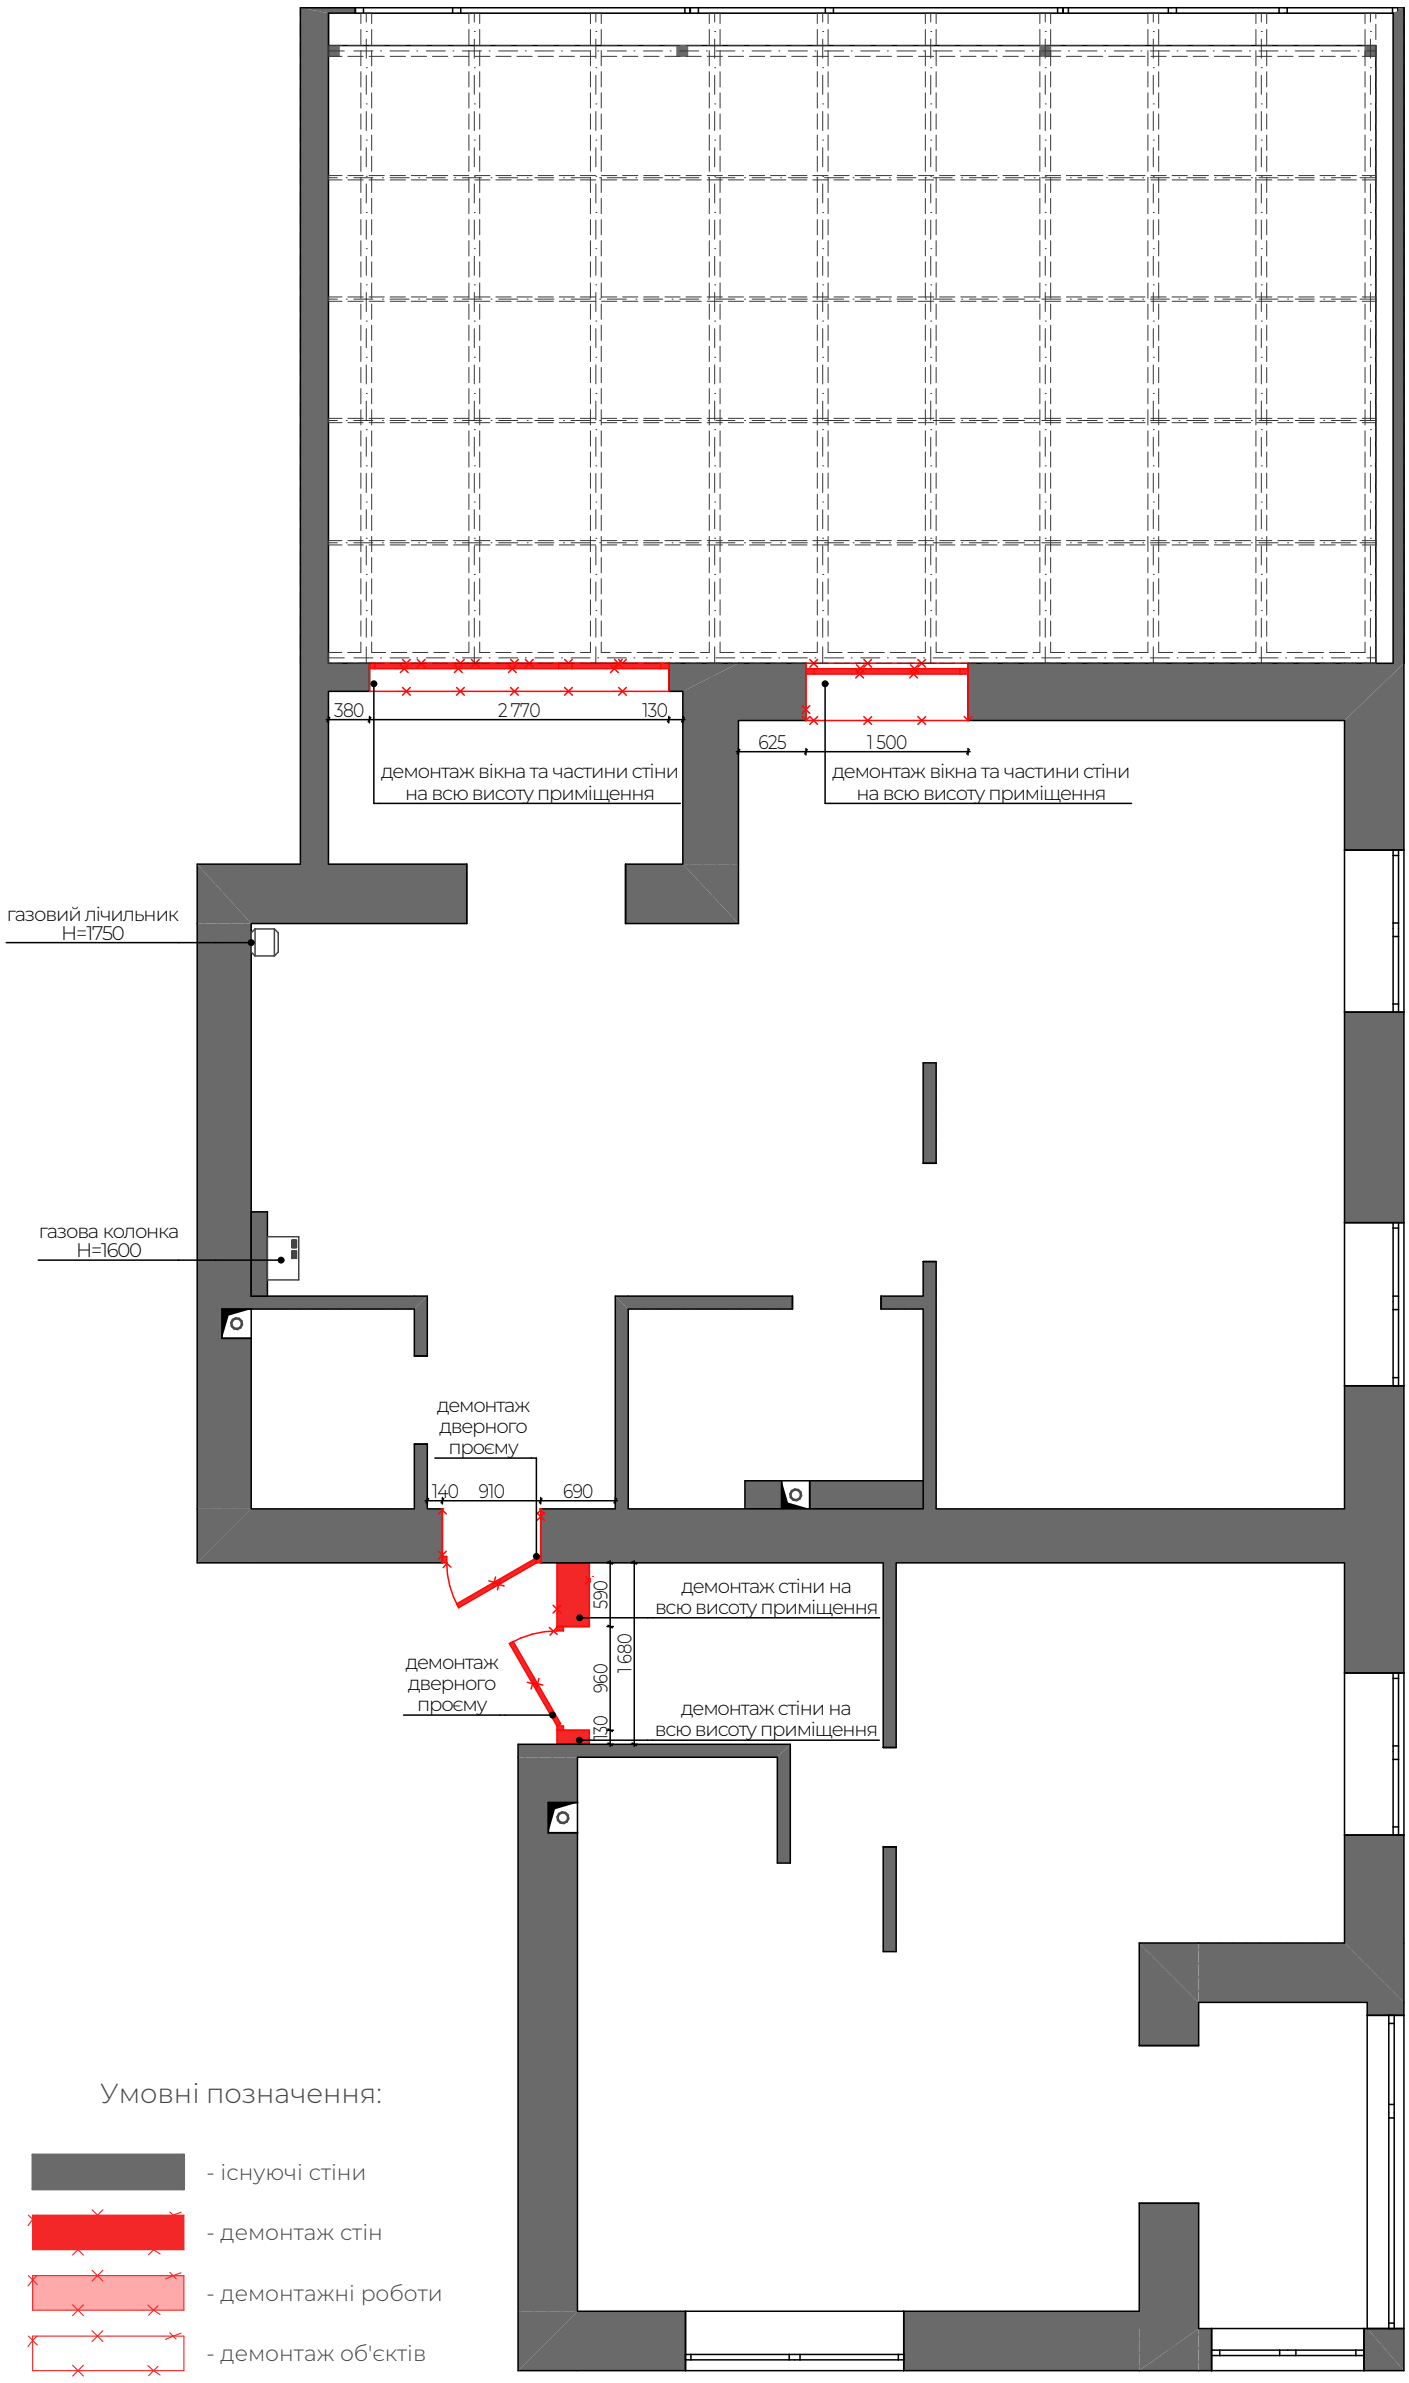

Примітки :
1. Зміст та загальні дані див. аркуш ДЗ-3.
2. Розміри приміщень після перепланування уточнити згідно арк. ДЗ-16.

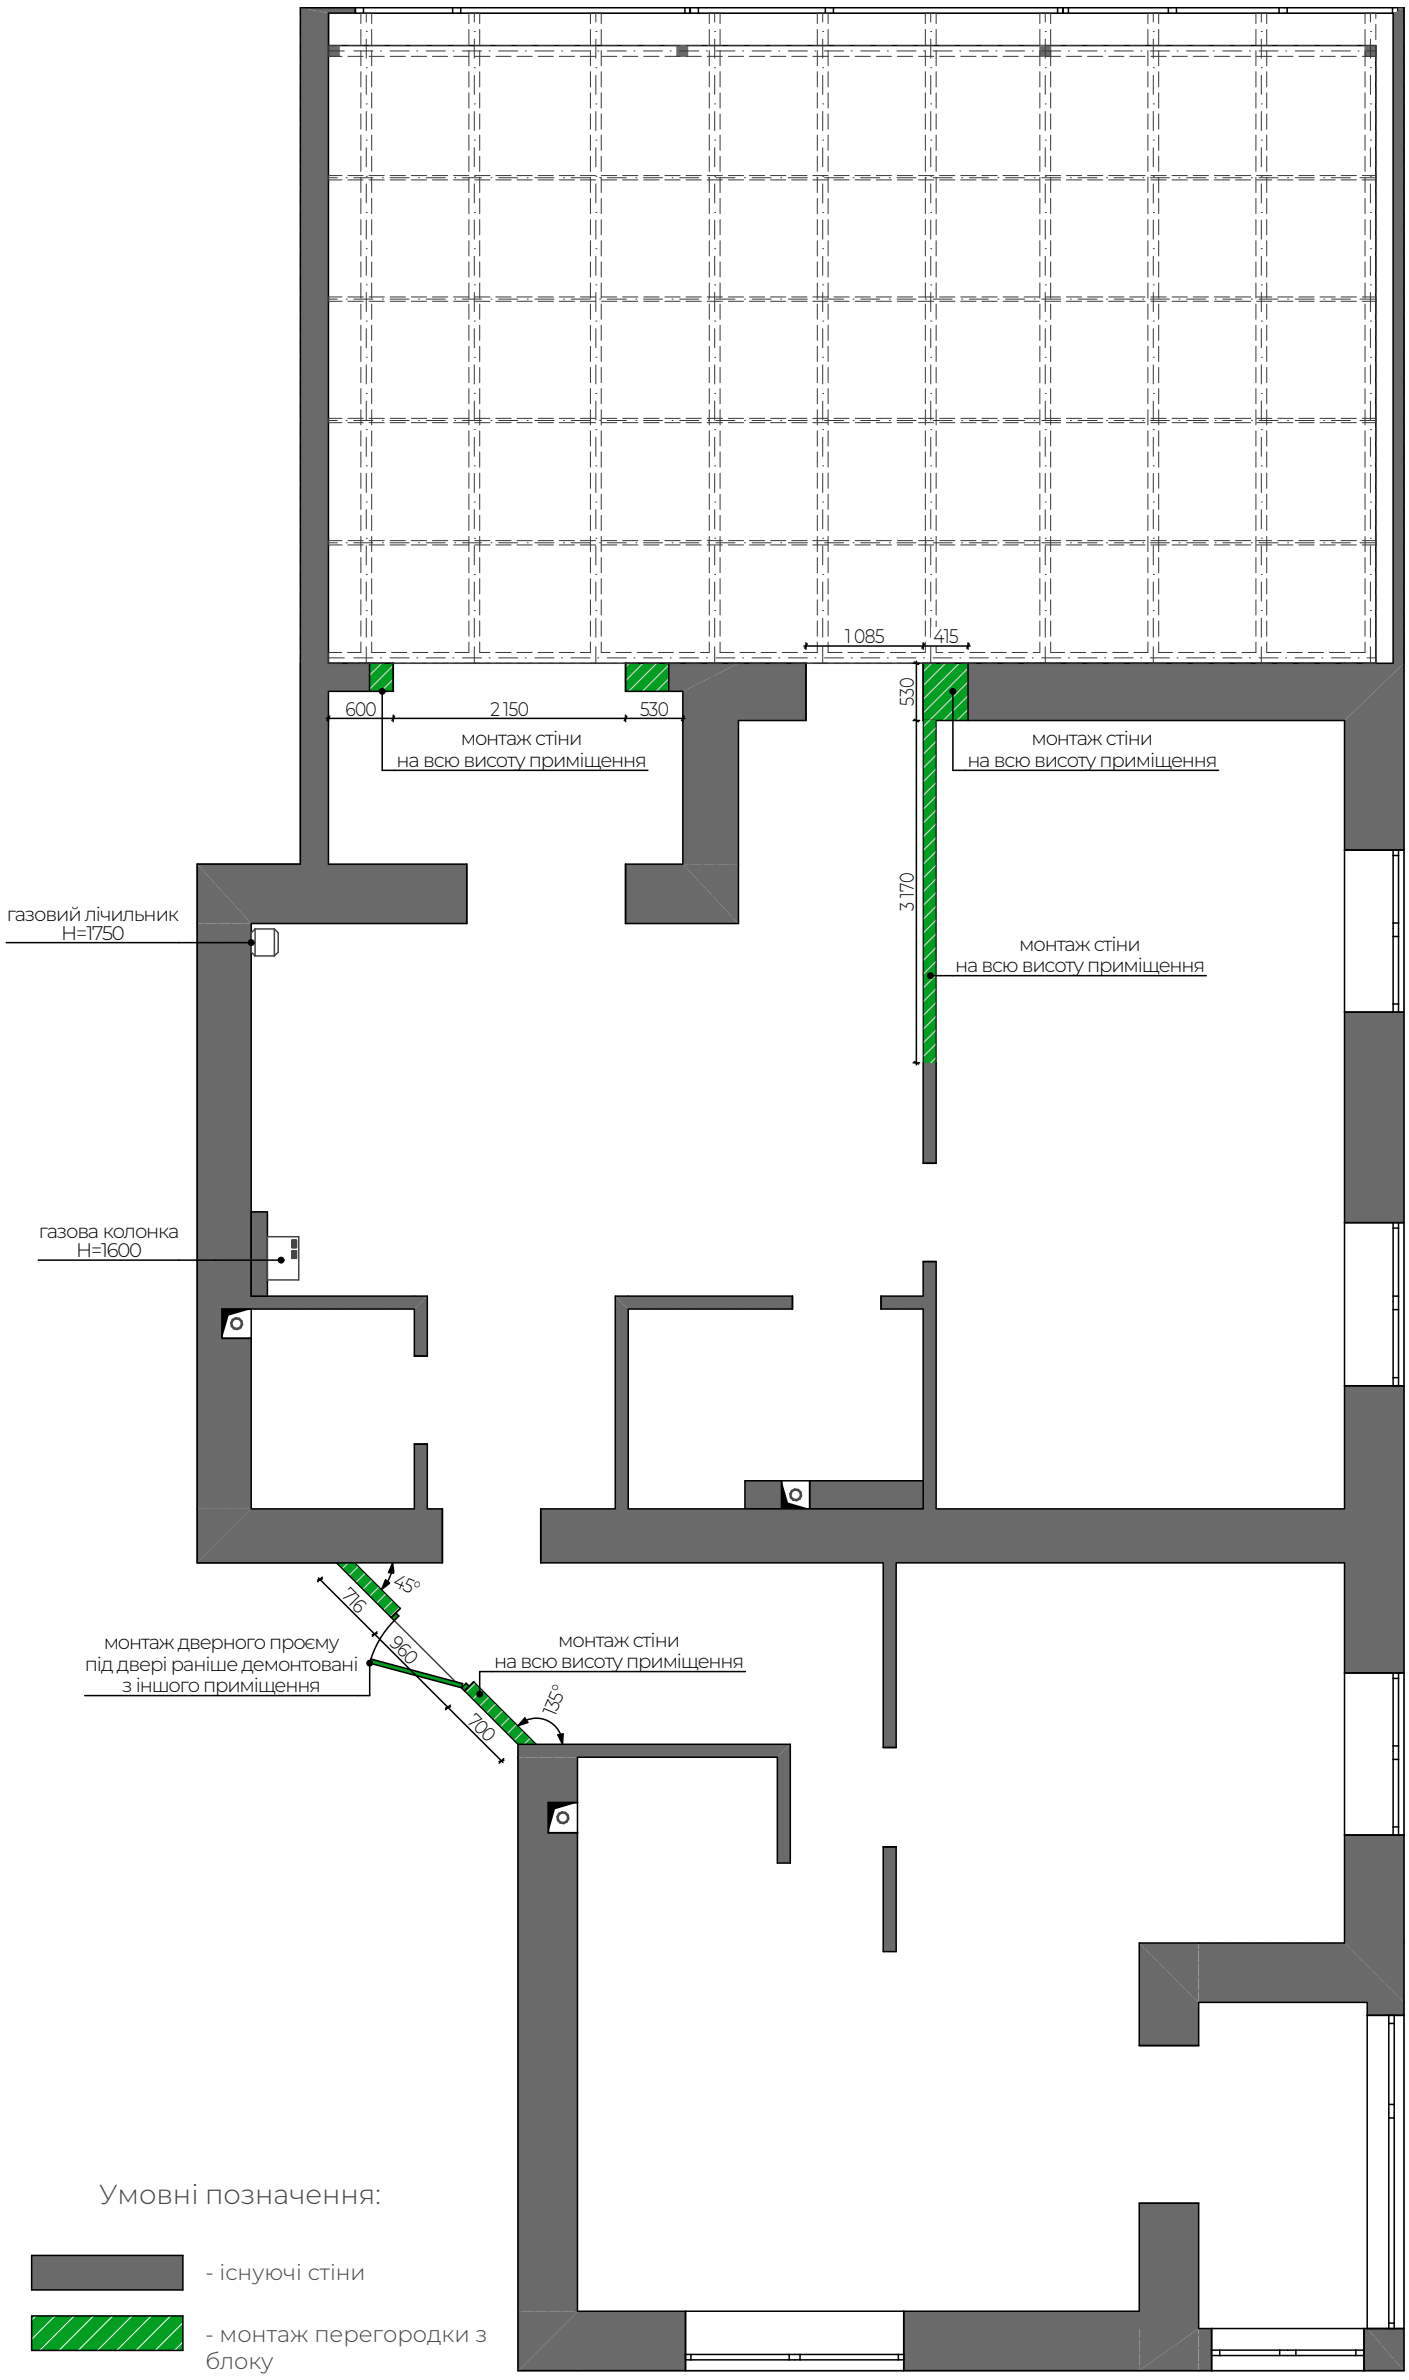

Примітки : 1. Товщини монтованих стін вказані без врахування вирівнювання стін.